

1 01 Ground Floor
1:50


DESIGN BY
D'PLUZ CONCEPTS
TECHNOLOGIES/
ENTERPRISE

08164342535

DRAWN BY:

ABDULQUDUS

A PROPOSED
4 BEDROOM
DUPLEX

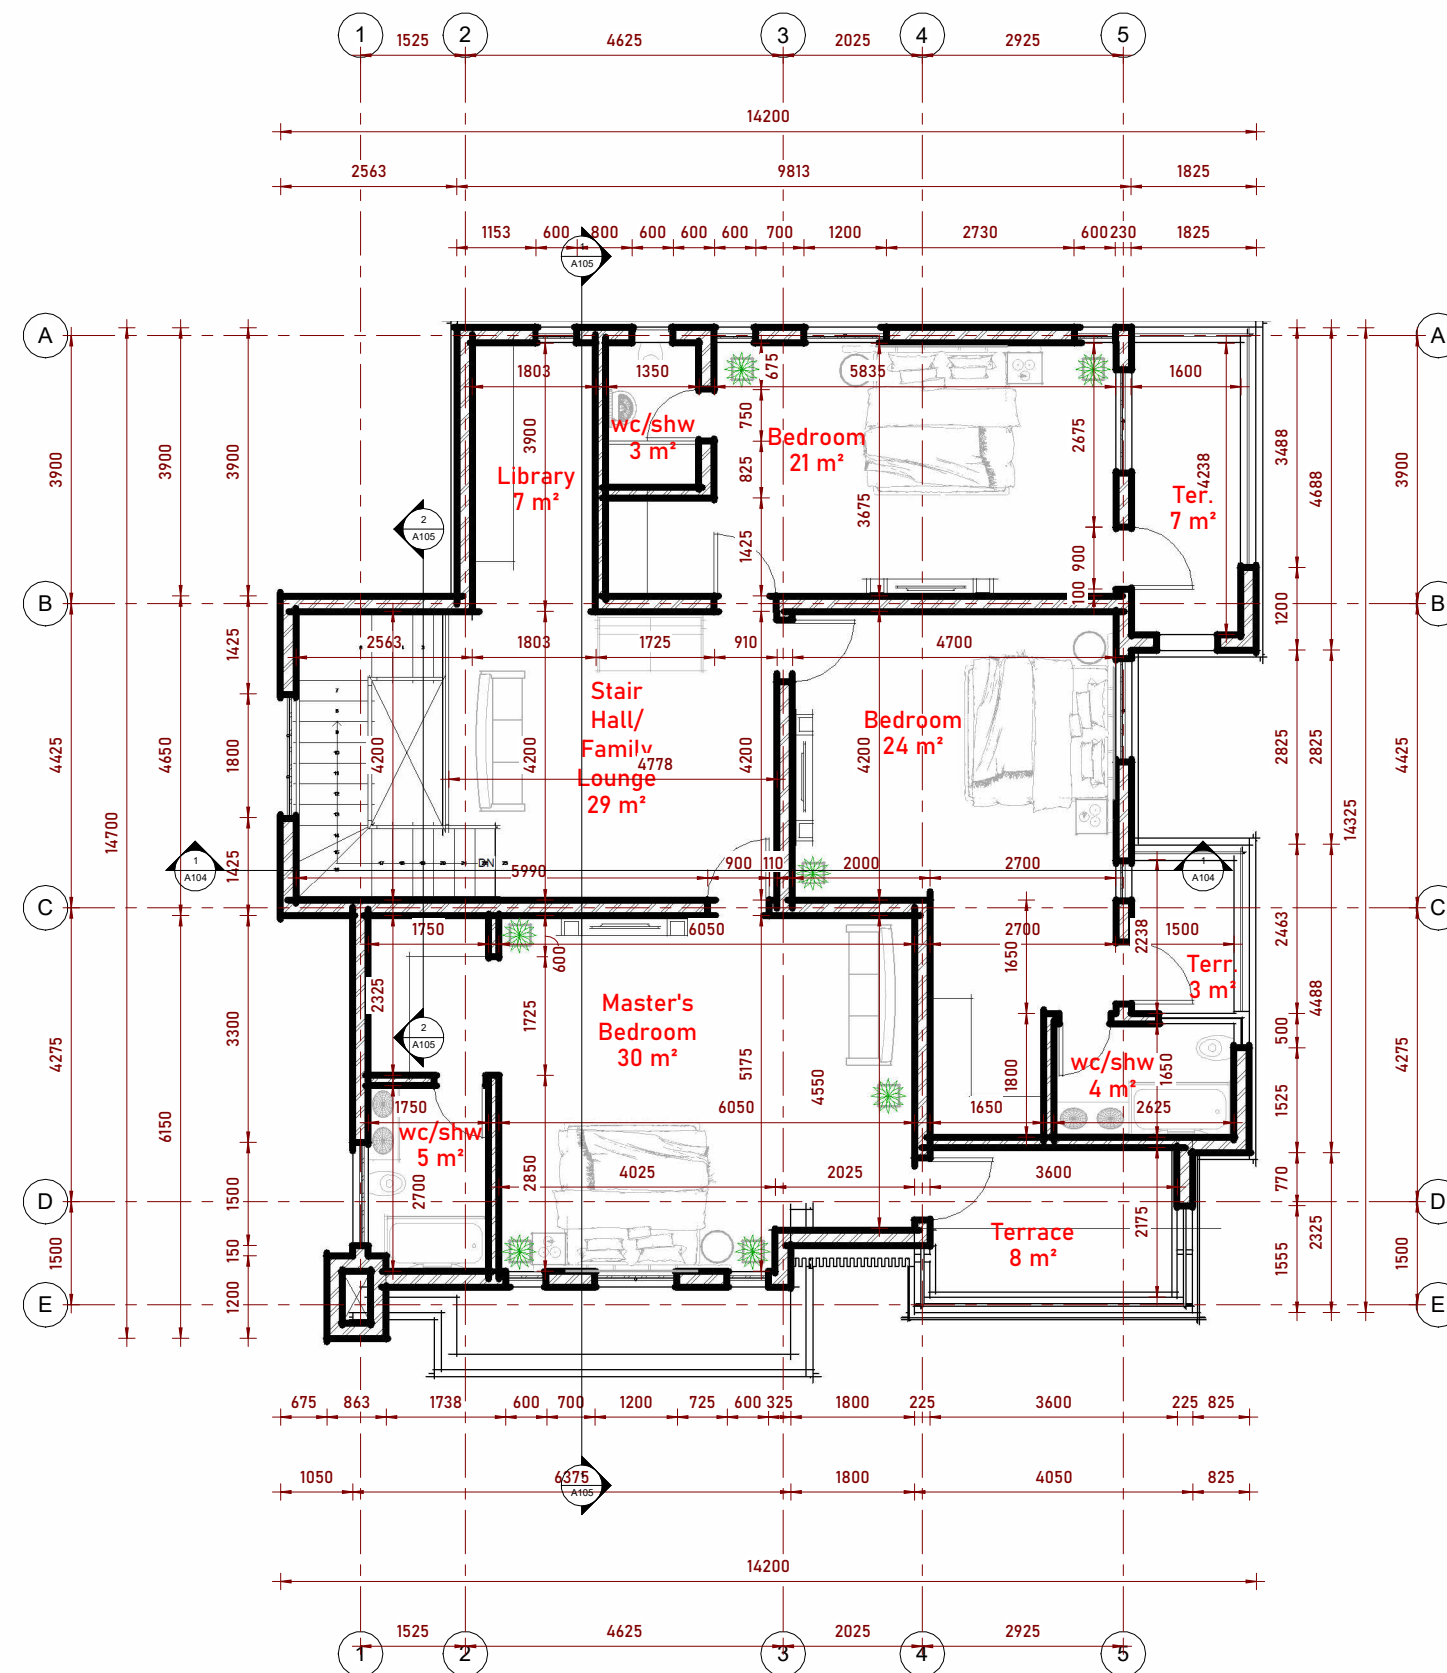

1 02 First Floor
1 : 50

DESIGN BY
D'PLUZ CONCEPTS
TECHNOLOGIES/
ENTERPRISE

08164342535

DRAWN BY:

ABDULQUDUS

A PROPOSED
4 BEDROOM
DUPLEX


DESIGN BY
D'PLUZ CONCEPTS
TECHNOLOGIES/
ENTERPRISE

08164342535

DRAWN BY:

ABDULQUDUS

**A PROPOSED
4 BEDROOM
DUPLEX**

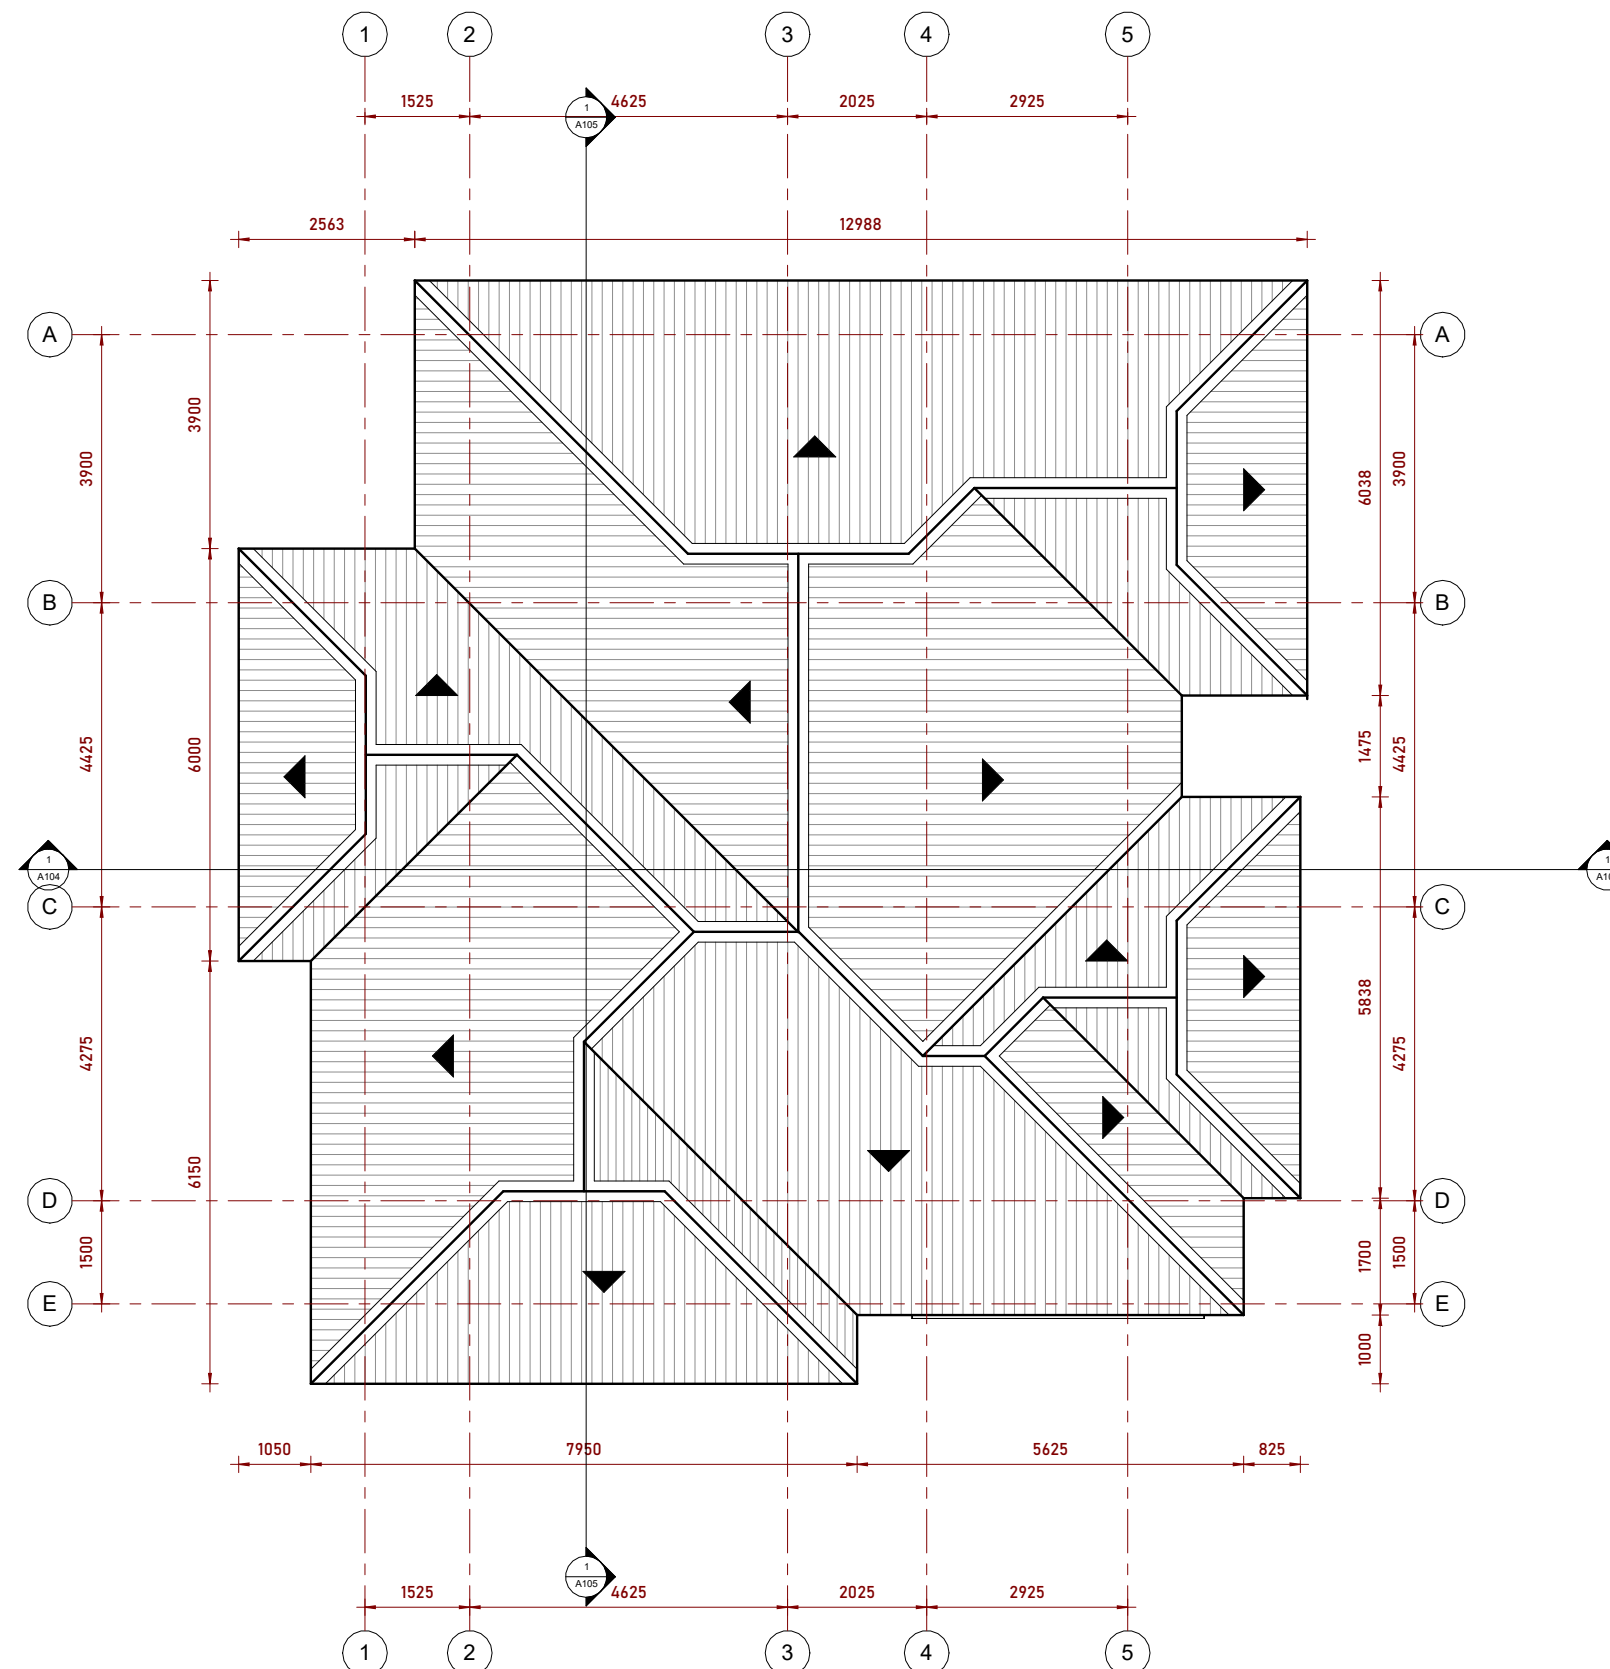

1 03 Roo Level
1 : 50


DESIGN BY
D'PLUZ CONCEPTS
TECHNOLOGIES/
ENTERPRISE

08164342535


DRAWN BY:

ABDULQUDUS

A PROPOSED
4 BEDROOM
DUPLEX

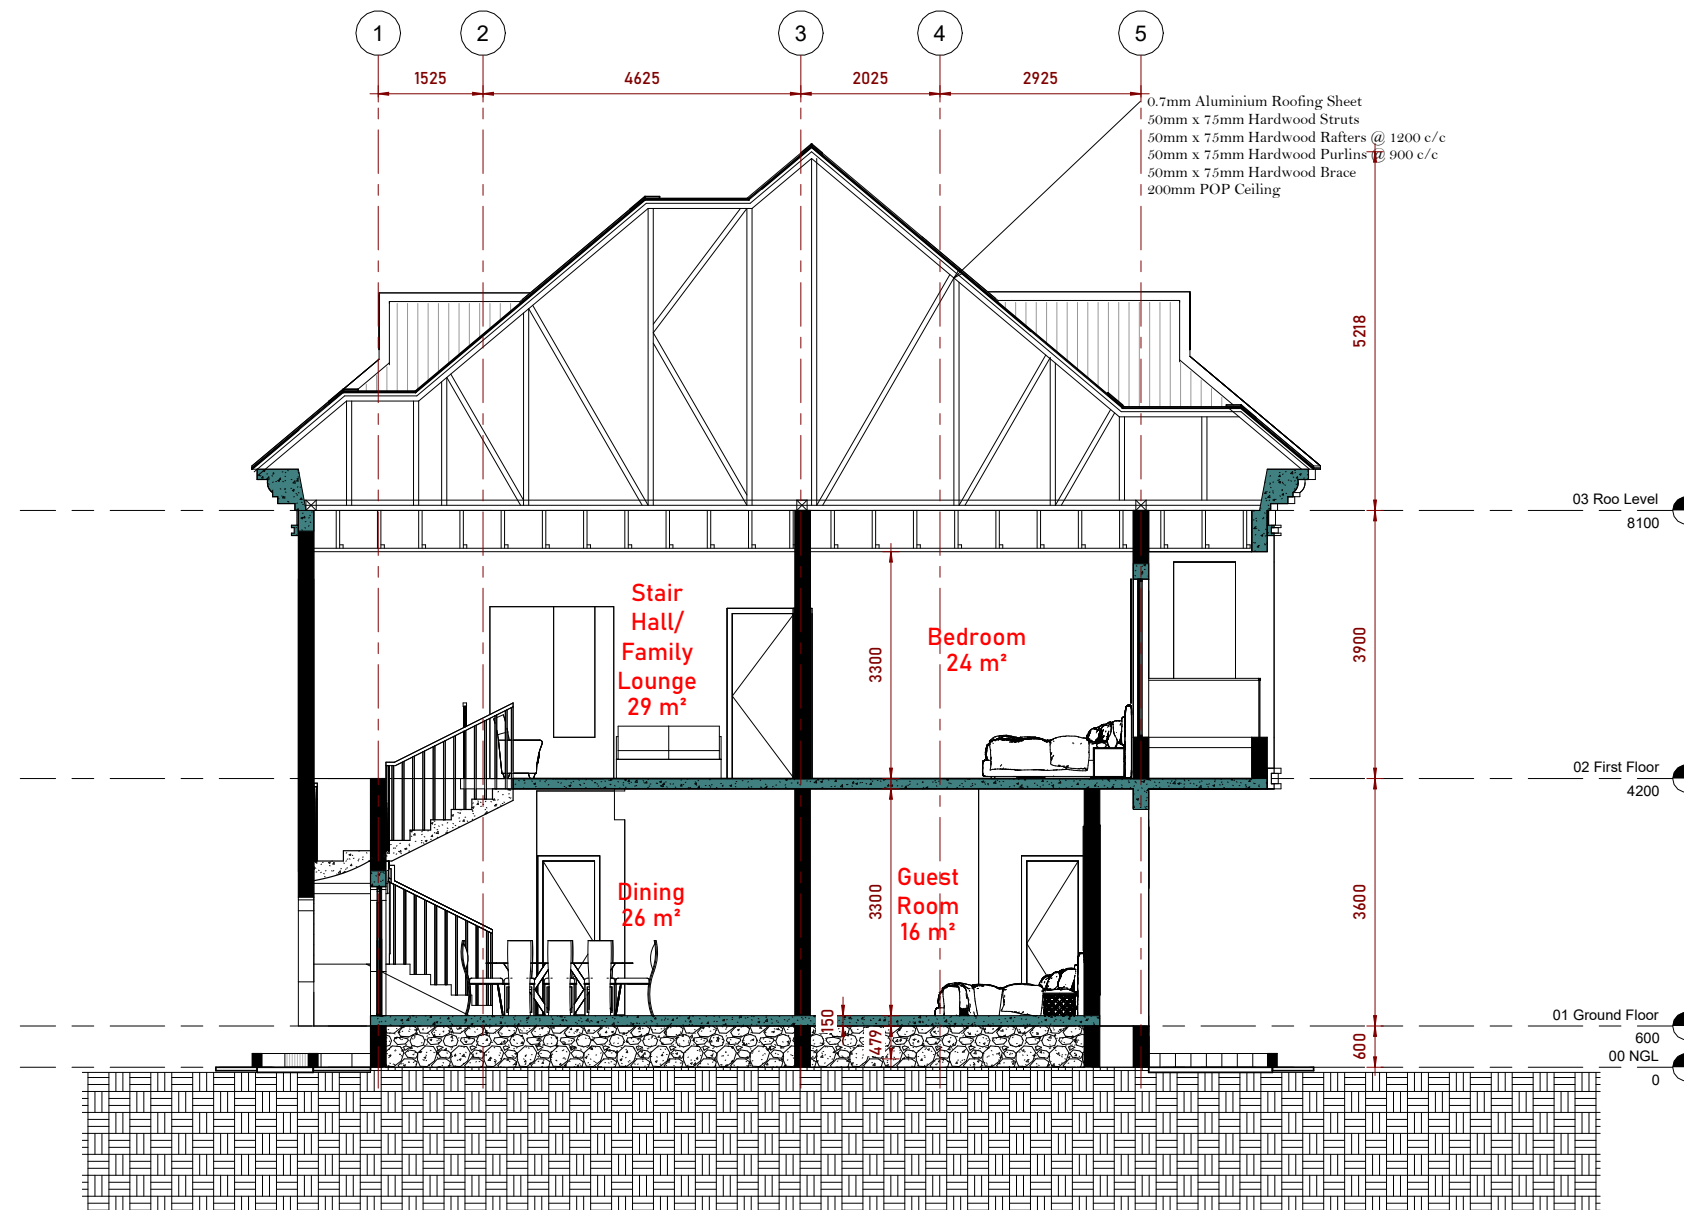

1 Section 1
1 : 50

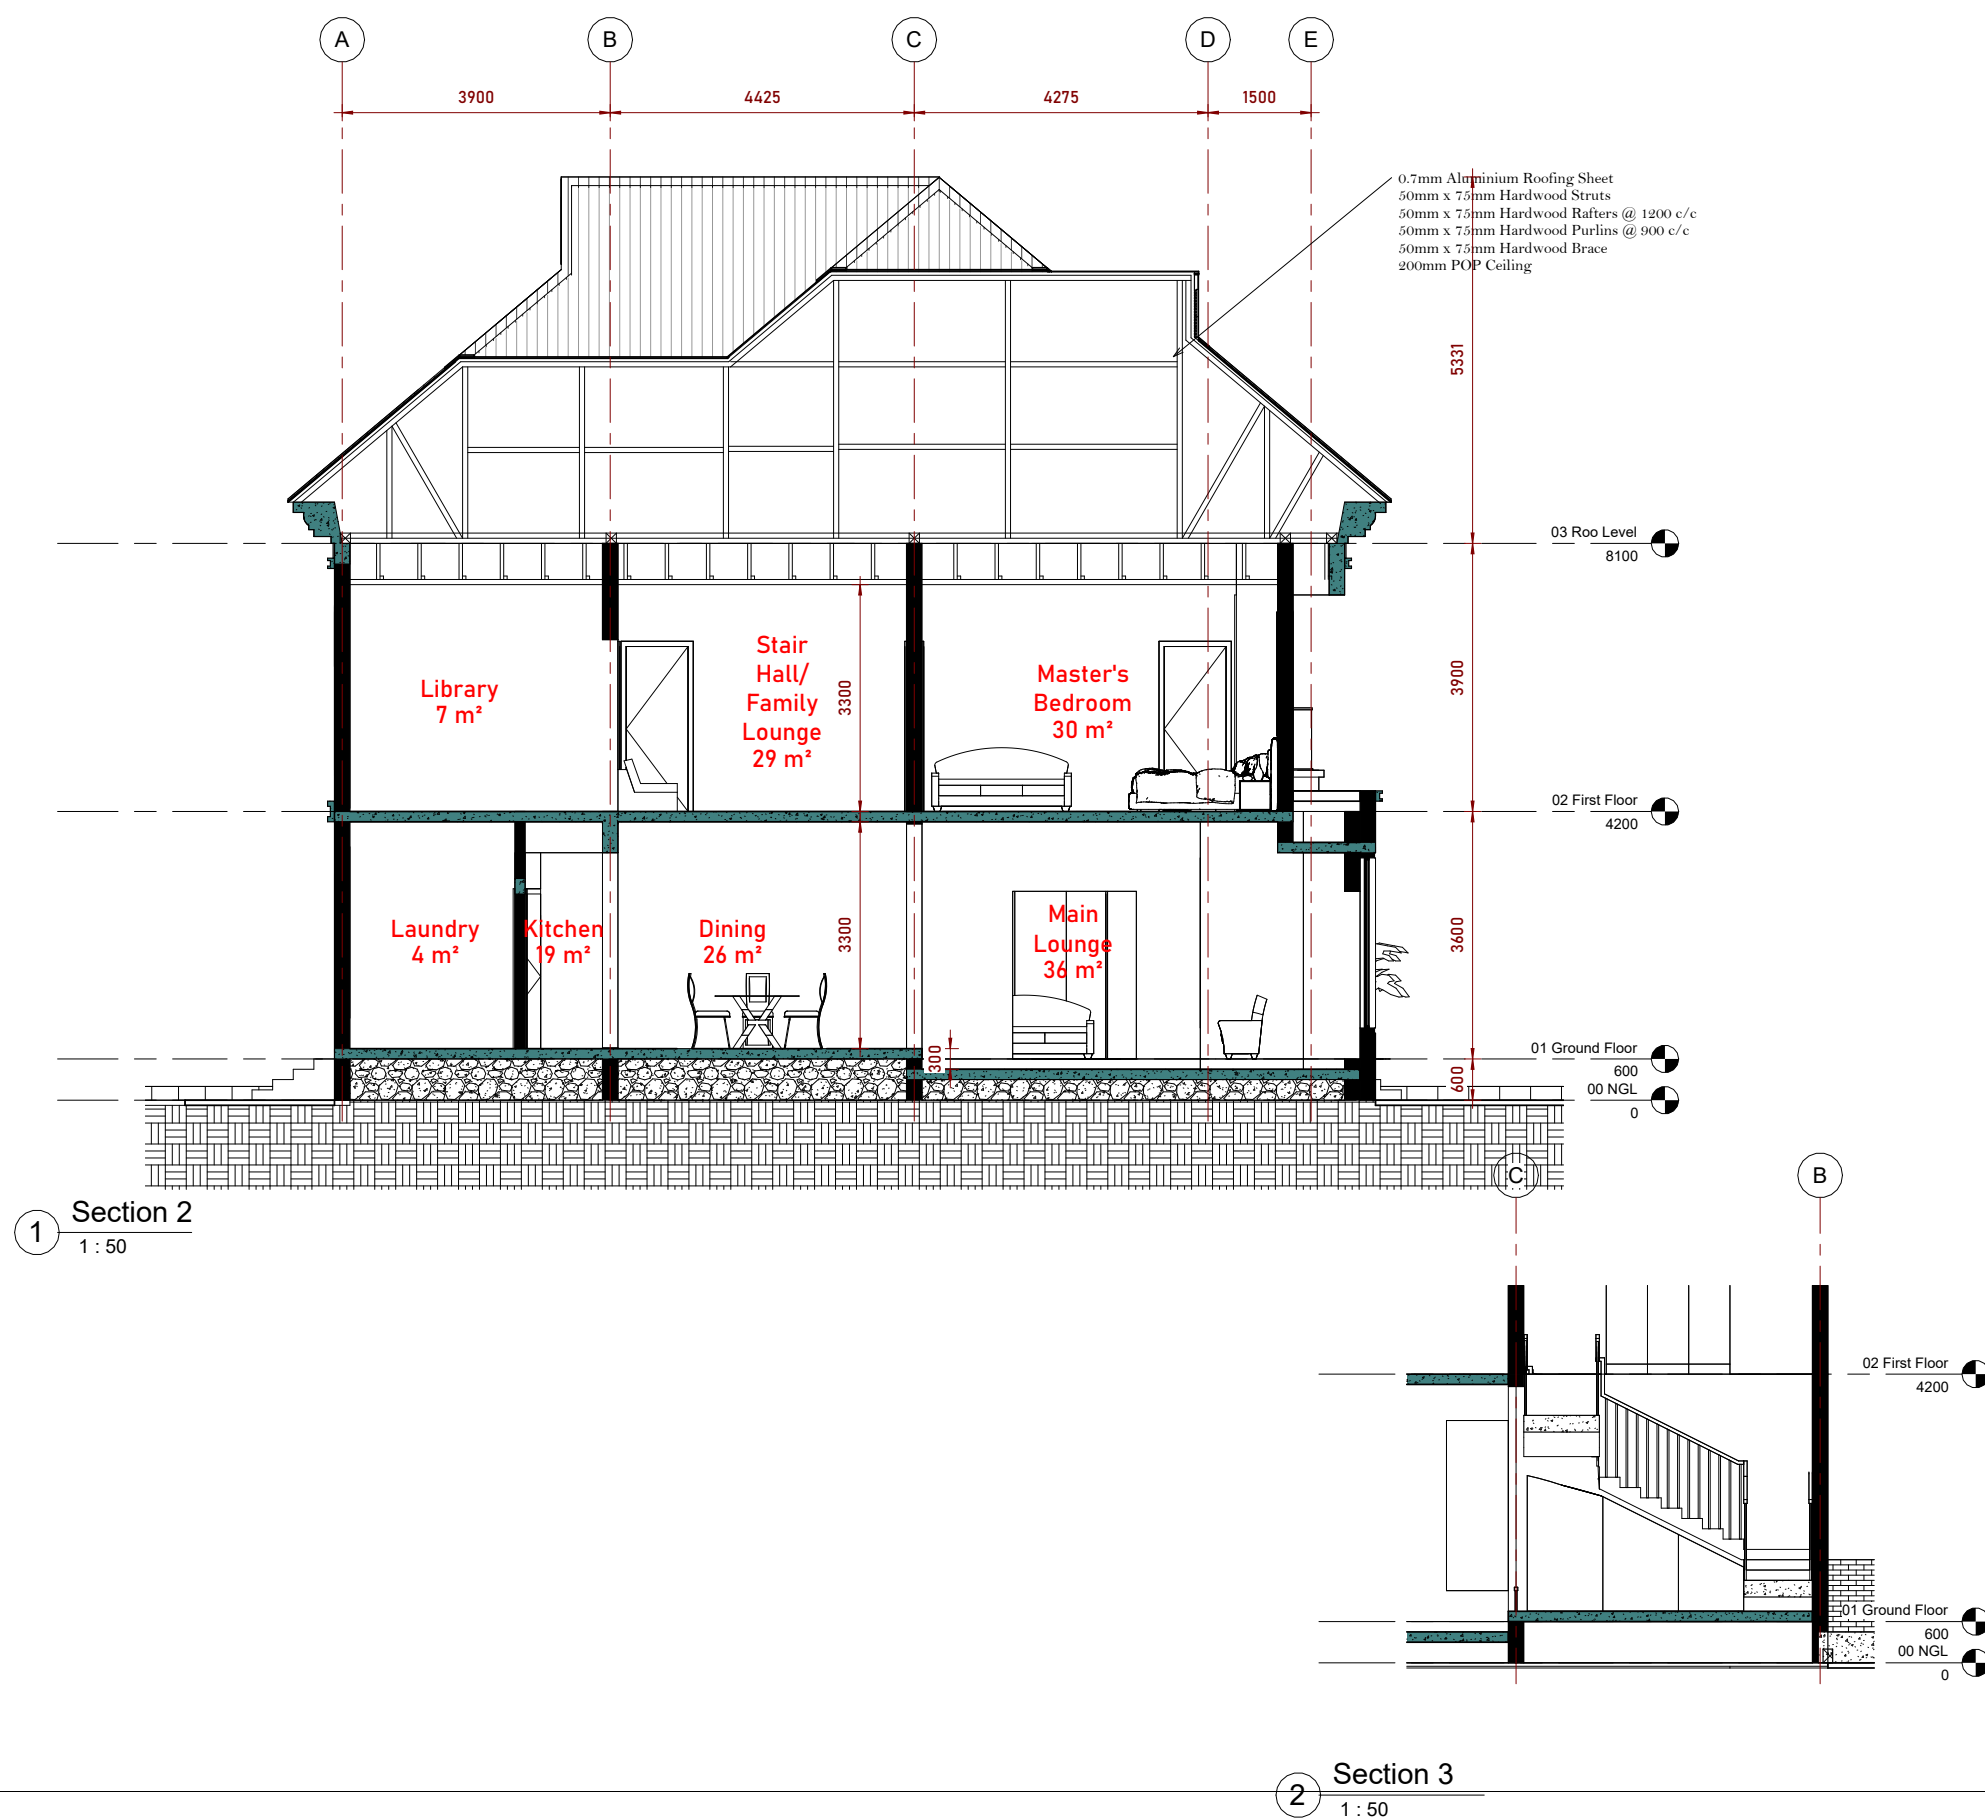

DESIGN BY
D'PLUZ CONCEPTS
TECHNOLOGIES/
ENTERPRISE

08164342535

DRAWN BY:
ABDULQUDUS

A PROPOSED
4 BEDROOM
DUPLEX

DESIGN BY
D'PLUZ CONCEPTS
TECHNOLOGIES/
ENTERPRISE

08164342535


DRAWN BY:

ABDULQUDUS

A PROPOSED
4 BEDROOM
DUPLEX



1 00 Approach View
1 : 50

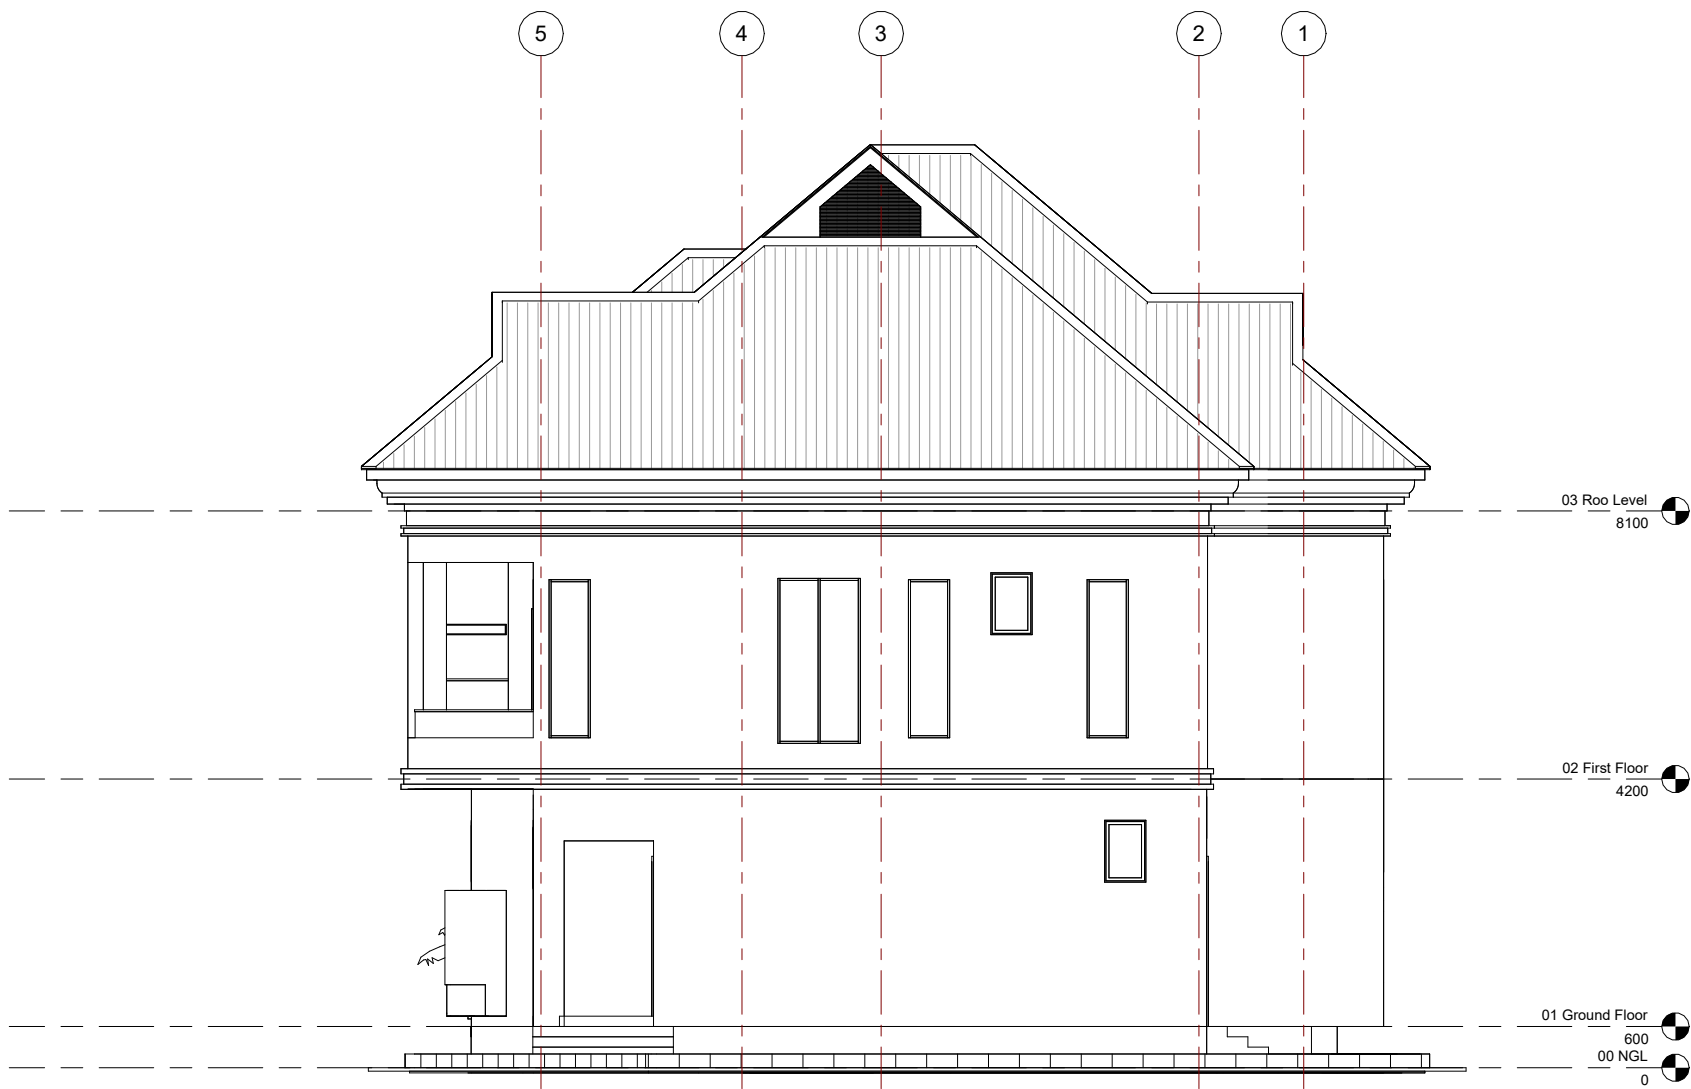

① 01 Rear Elevation
1 : 50

DESIGN BY
D'PLUZ CONCEPTS
TECHNOLOGIES/
ENTERPRISE

08164342535

DRAWN BY:

ABDULQUDUS

A PROPOSED
4 BEDROOM
DUPLEX

DESIGN BY
D'PLUZ CONCEPTS
TECHNOLOGIES/
ENTERPRISE

08164342535

DRAWN BY:

ABDULQUDUS

A PROPOSED
4 BEDROOM
DUPLEX

WOODEN PANEL DOOR (D-01) 900X2100mm		WOODEN PANEL DOOR (D-02) 750X2100mm		D ₃ SWISS SECURITY DOOR (D-03) 2100X2100mm	
DOOR DESCRIPTION	Single leaf wooden panel door installed with mortise lock & Architrave on both side	DOOR DESCRIPTION	Single Leaf Wooden internal door installed with mortise lock & Architrave on both sides	DOOR DESCRIPTION	Double Leaf Swiss Security steel door installed with mortise lock & Architrave on both sides
No(s)	09 3608	No(s)	06	No(s)	01



Door Schedule
1 : 25

DESIGN BY
D'PLUZ CONCEPTS
TECHNOLOGIES/
ENTERPRISE


08164342535

DRAWN BY:

ABDULQUDUS

A PROPOSED
4 BEDROOM
DUPLEX



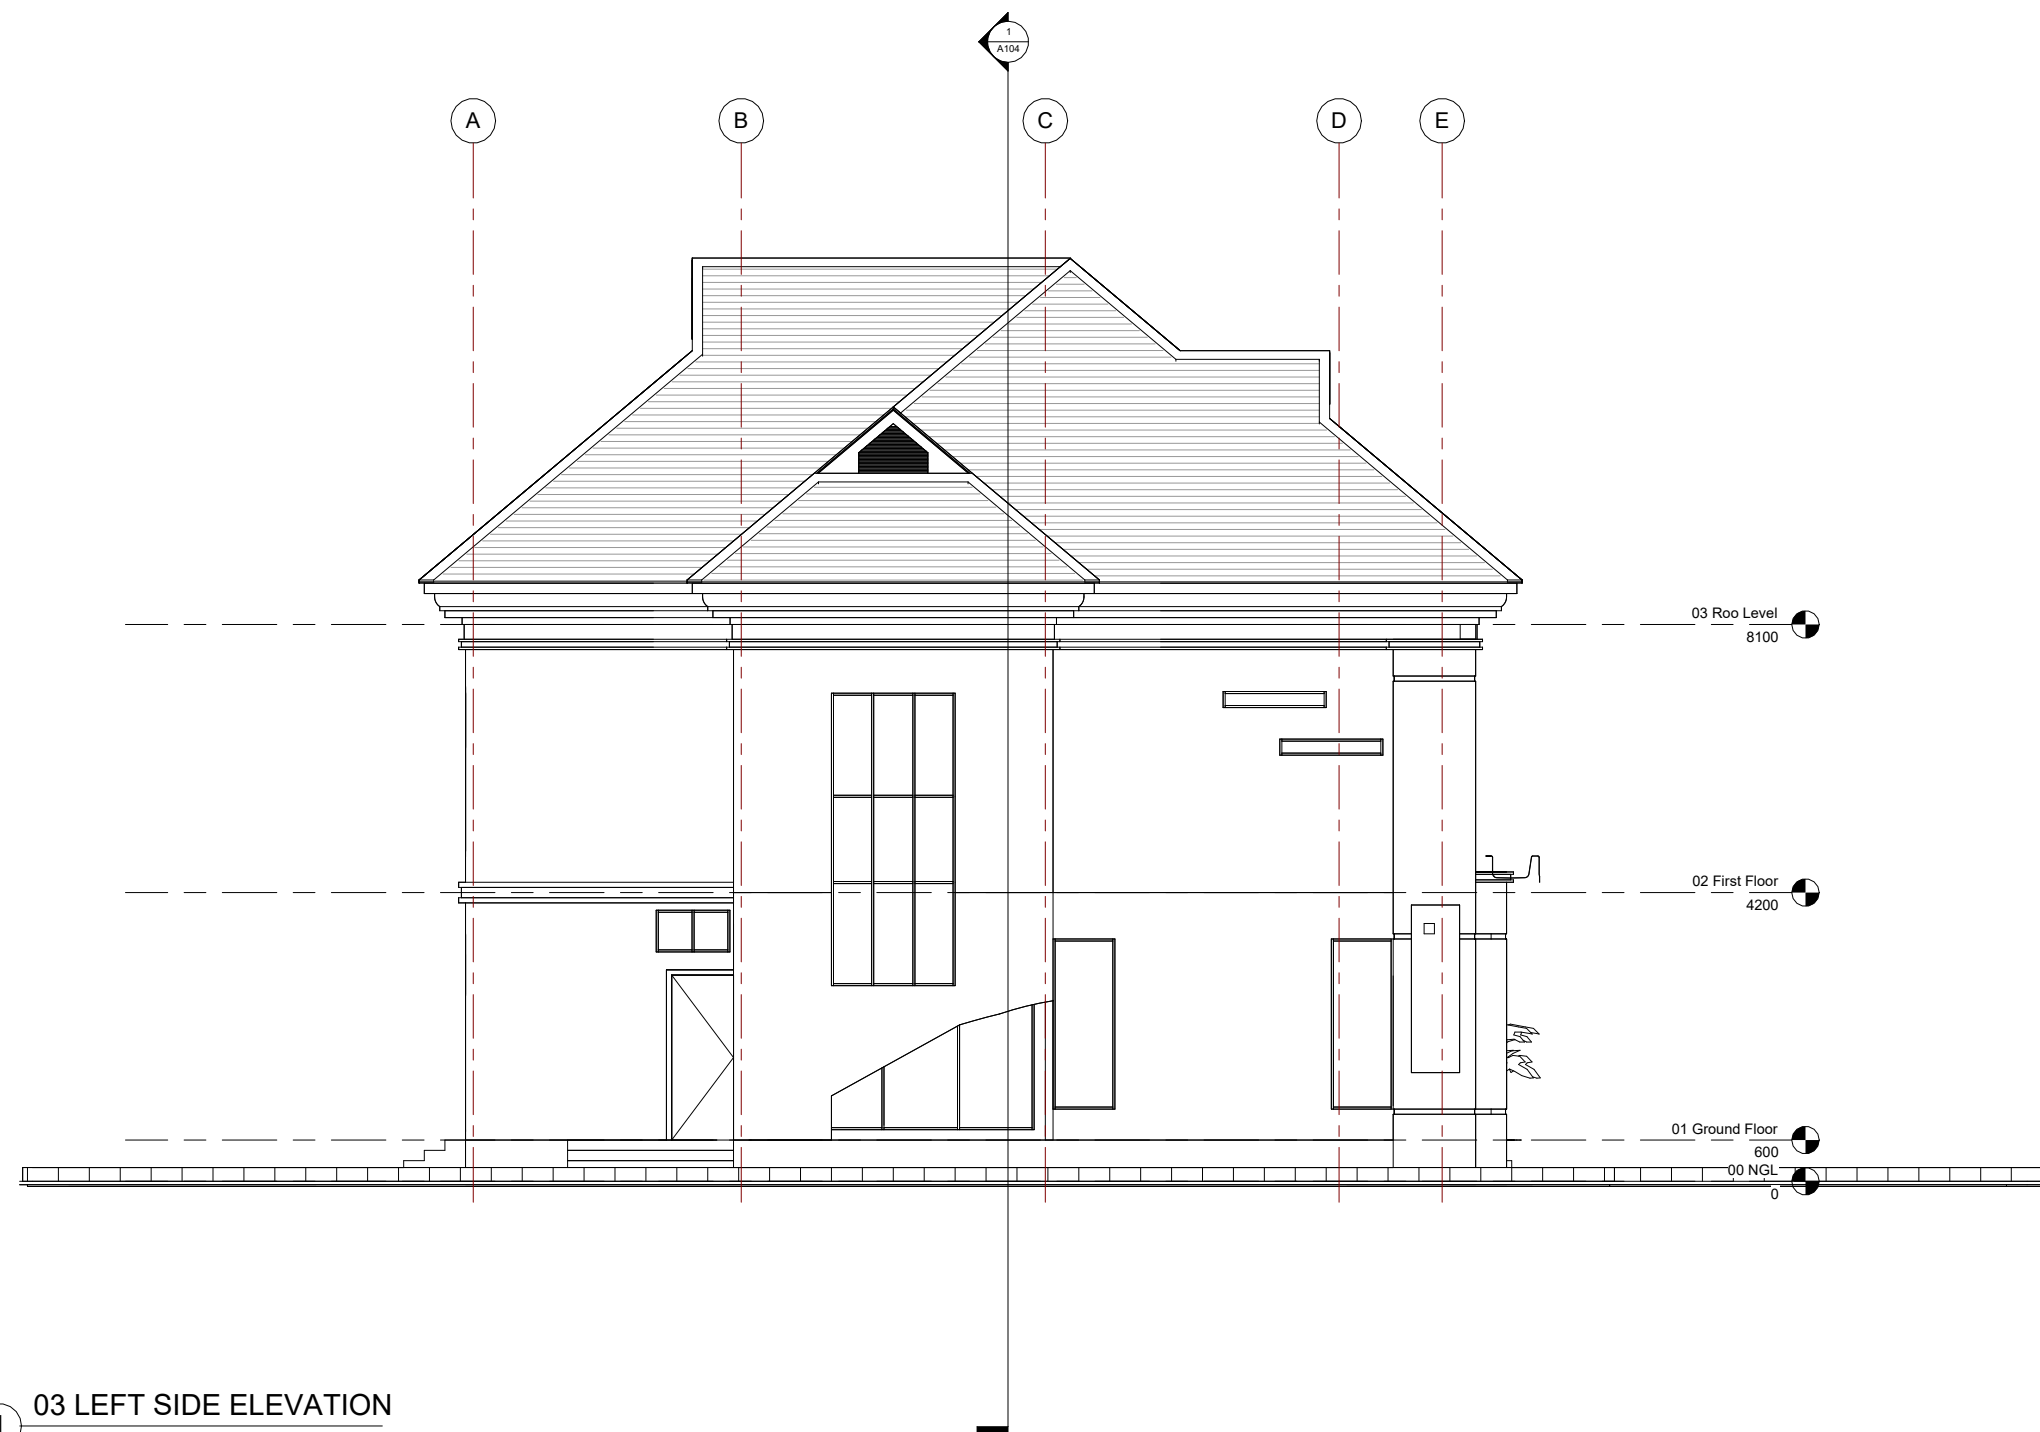

1 03 LEFT SIDE ELEVATION
1:50

DESIGN BY
D'PLUZ CONCEPTS
TECHNOLOGIES/
ENTERPRISE

08164342535

DRAWN BY:

ABDULQUDUS

A PROPOSED
4 BEDROOM
DUPLEX



DESIGN BY
D'PLUZ CONCEPTS
TECHNOLOGIES/
ENTERPRISE

08164342535

DRAWN BY:

ABDULQUDUS

**A PROPOSED
4 BEDROOM
DUPLEX**

DESIGN BY
D'PLUZ CONCEPTS
TECHNOLOGIES/
ENTERPRISE

08164342535

DRAWN BY:

ABDULQUDUS

A PROPOSED
4 BEDROOM
DUPLEX





DESIGN BY
D'PLUZ CONCEPTS
TECHNOLOGIES/
ENTERPRISE

08164342535

DRAWN BY:
ABDULQUDUS

A PROPOSED
4 BEDROOM
DUPLEX