




1 01 Ground Floor  
1 : 50

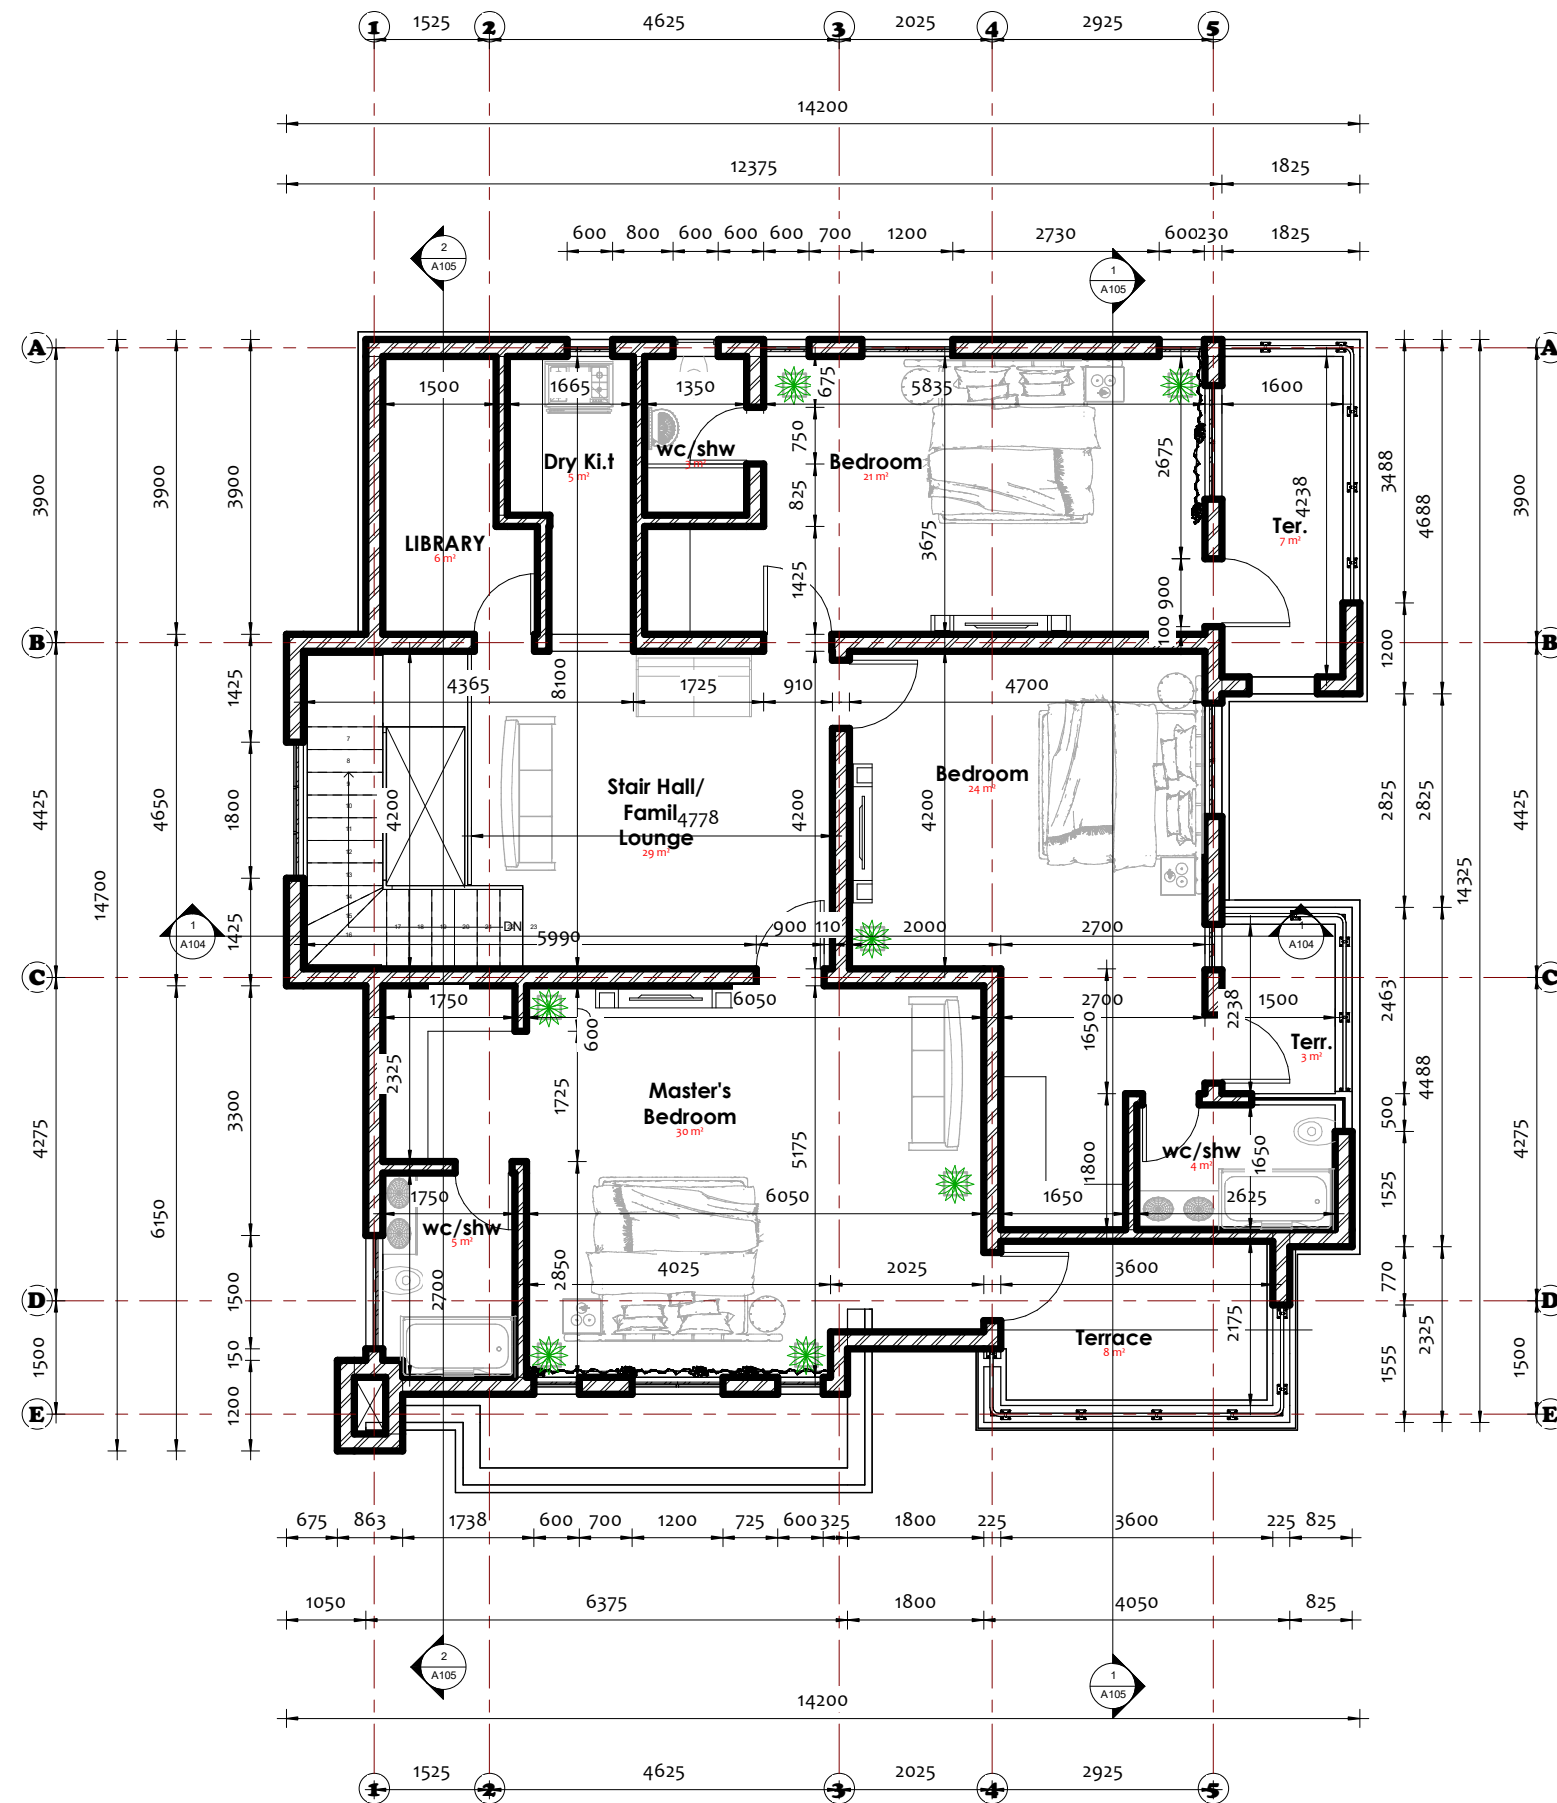


1 02 First Floor  
1 : 50

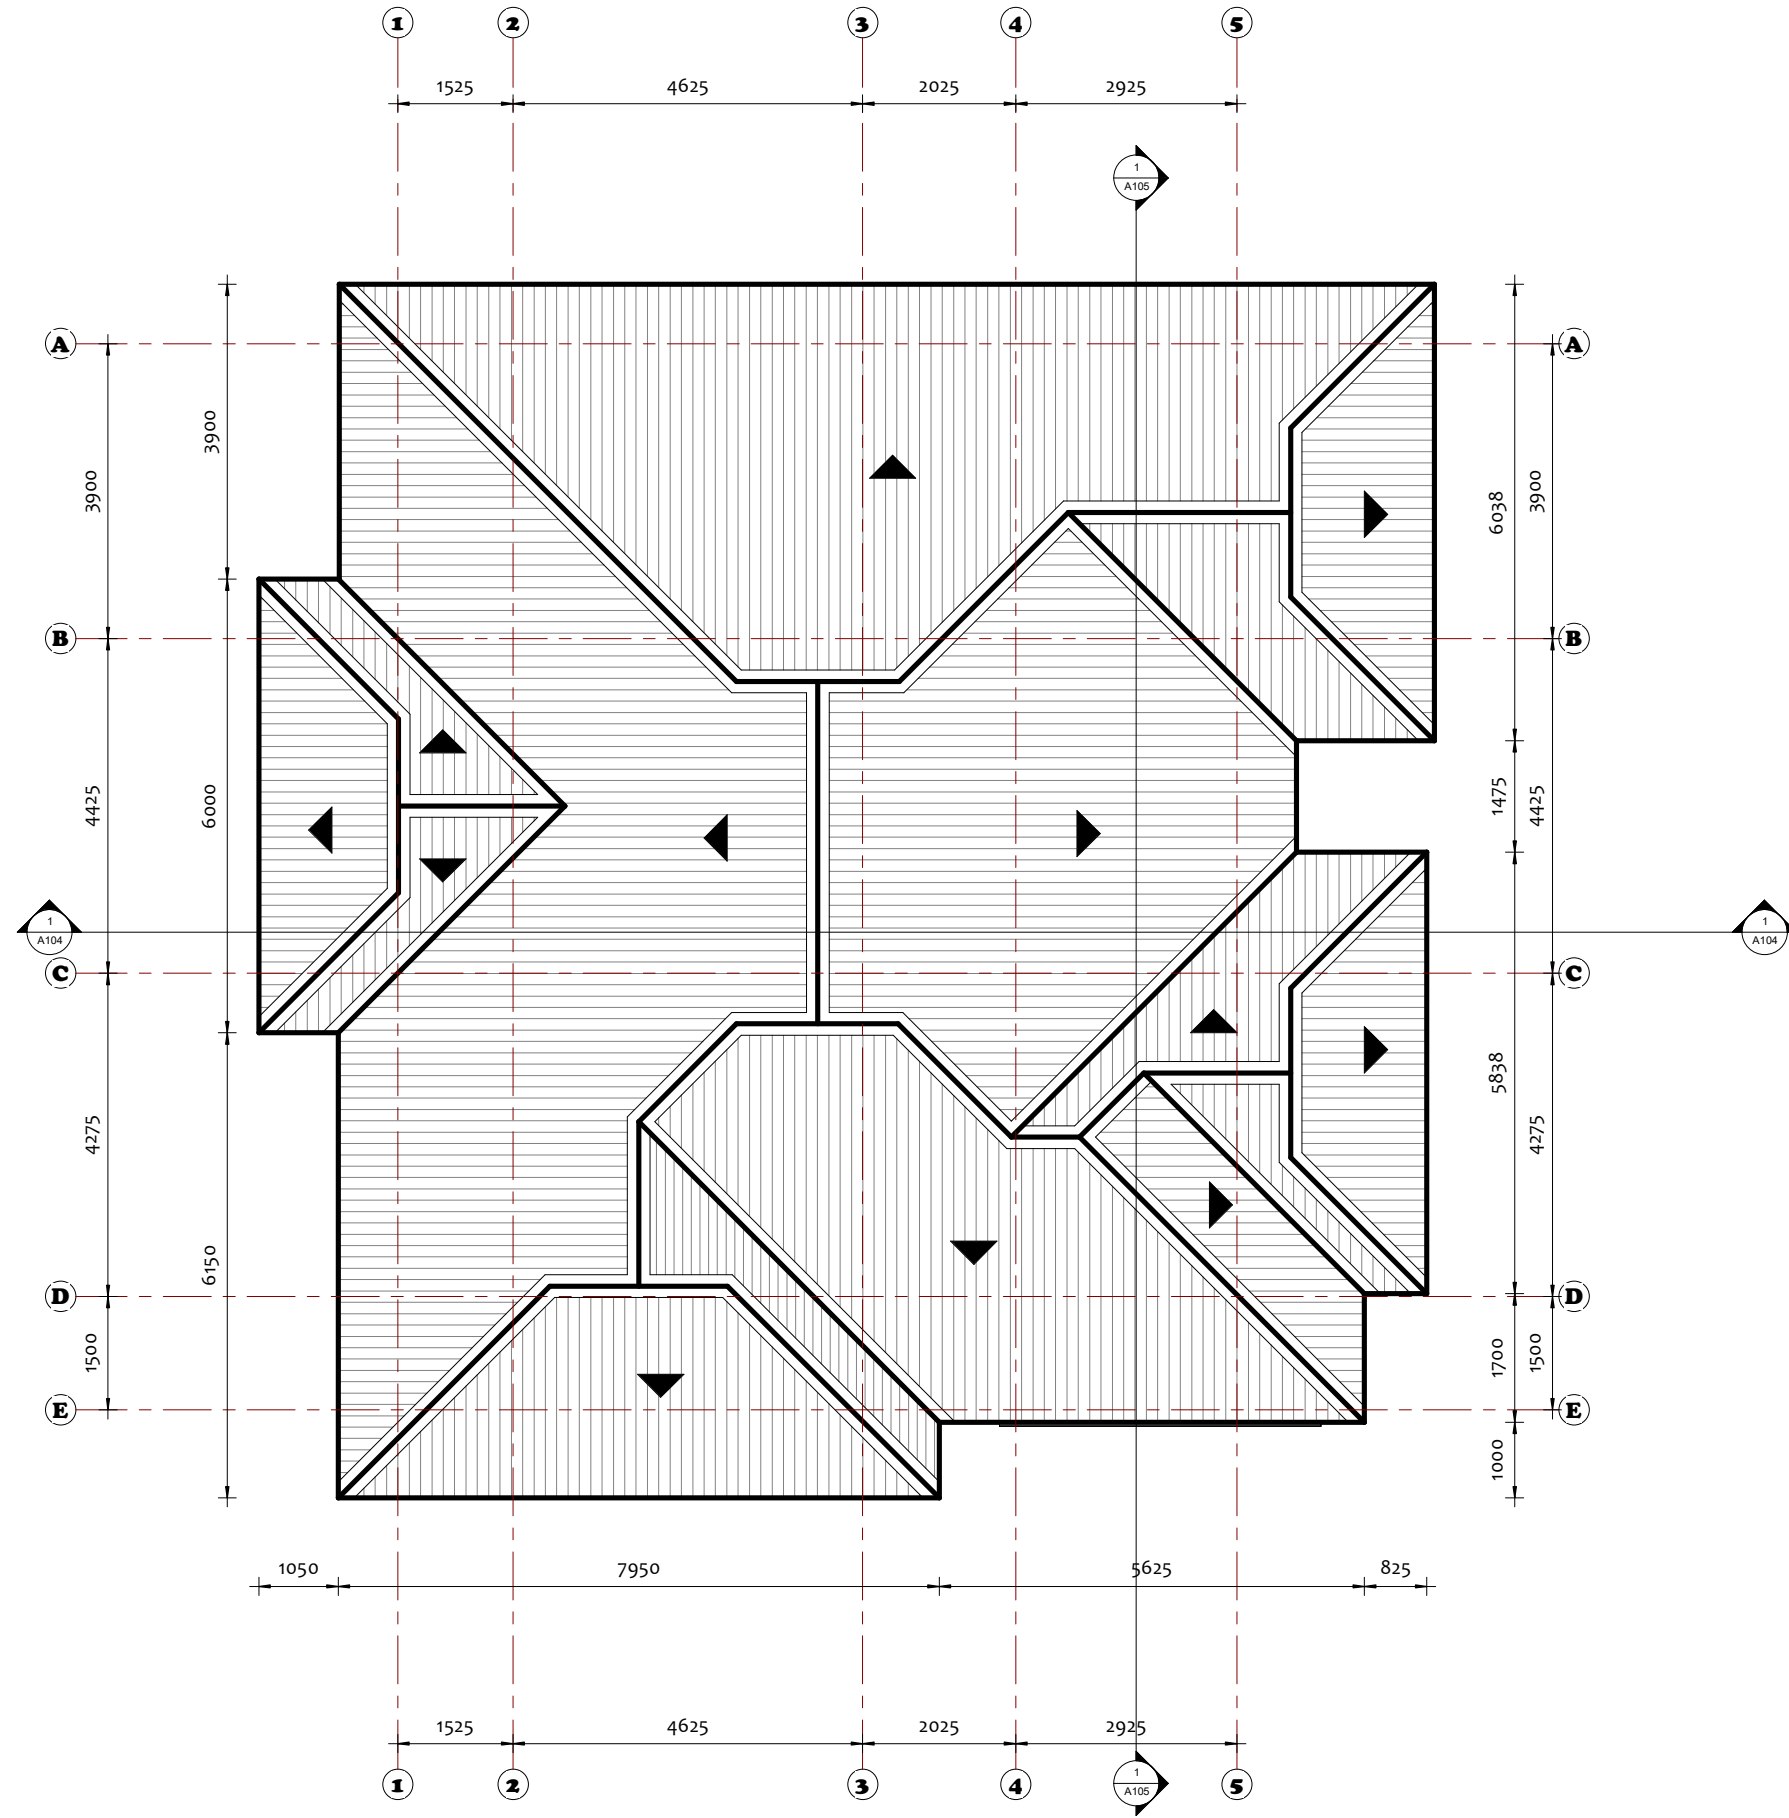


1 03 Roo Level  
1 : 50

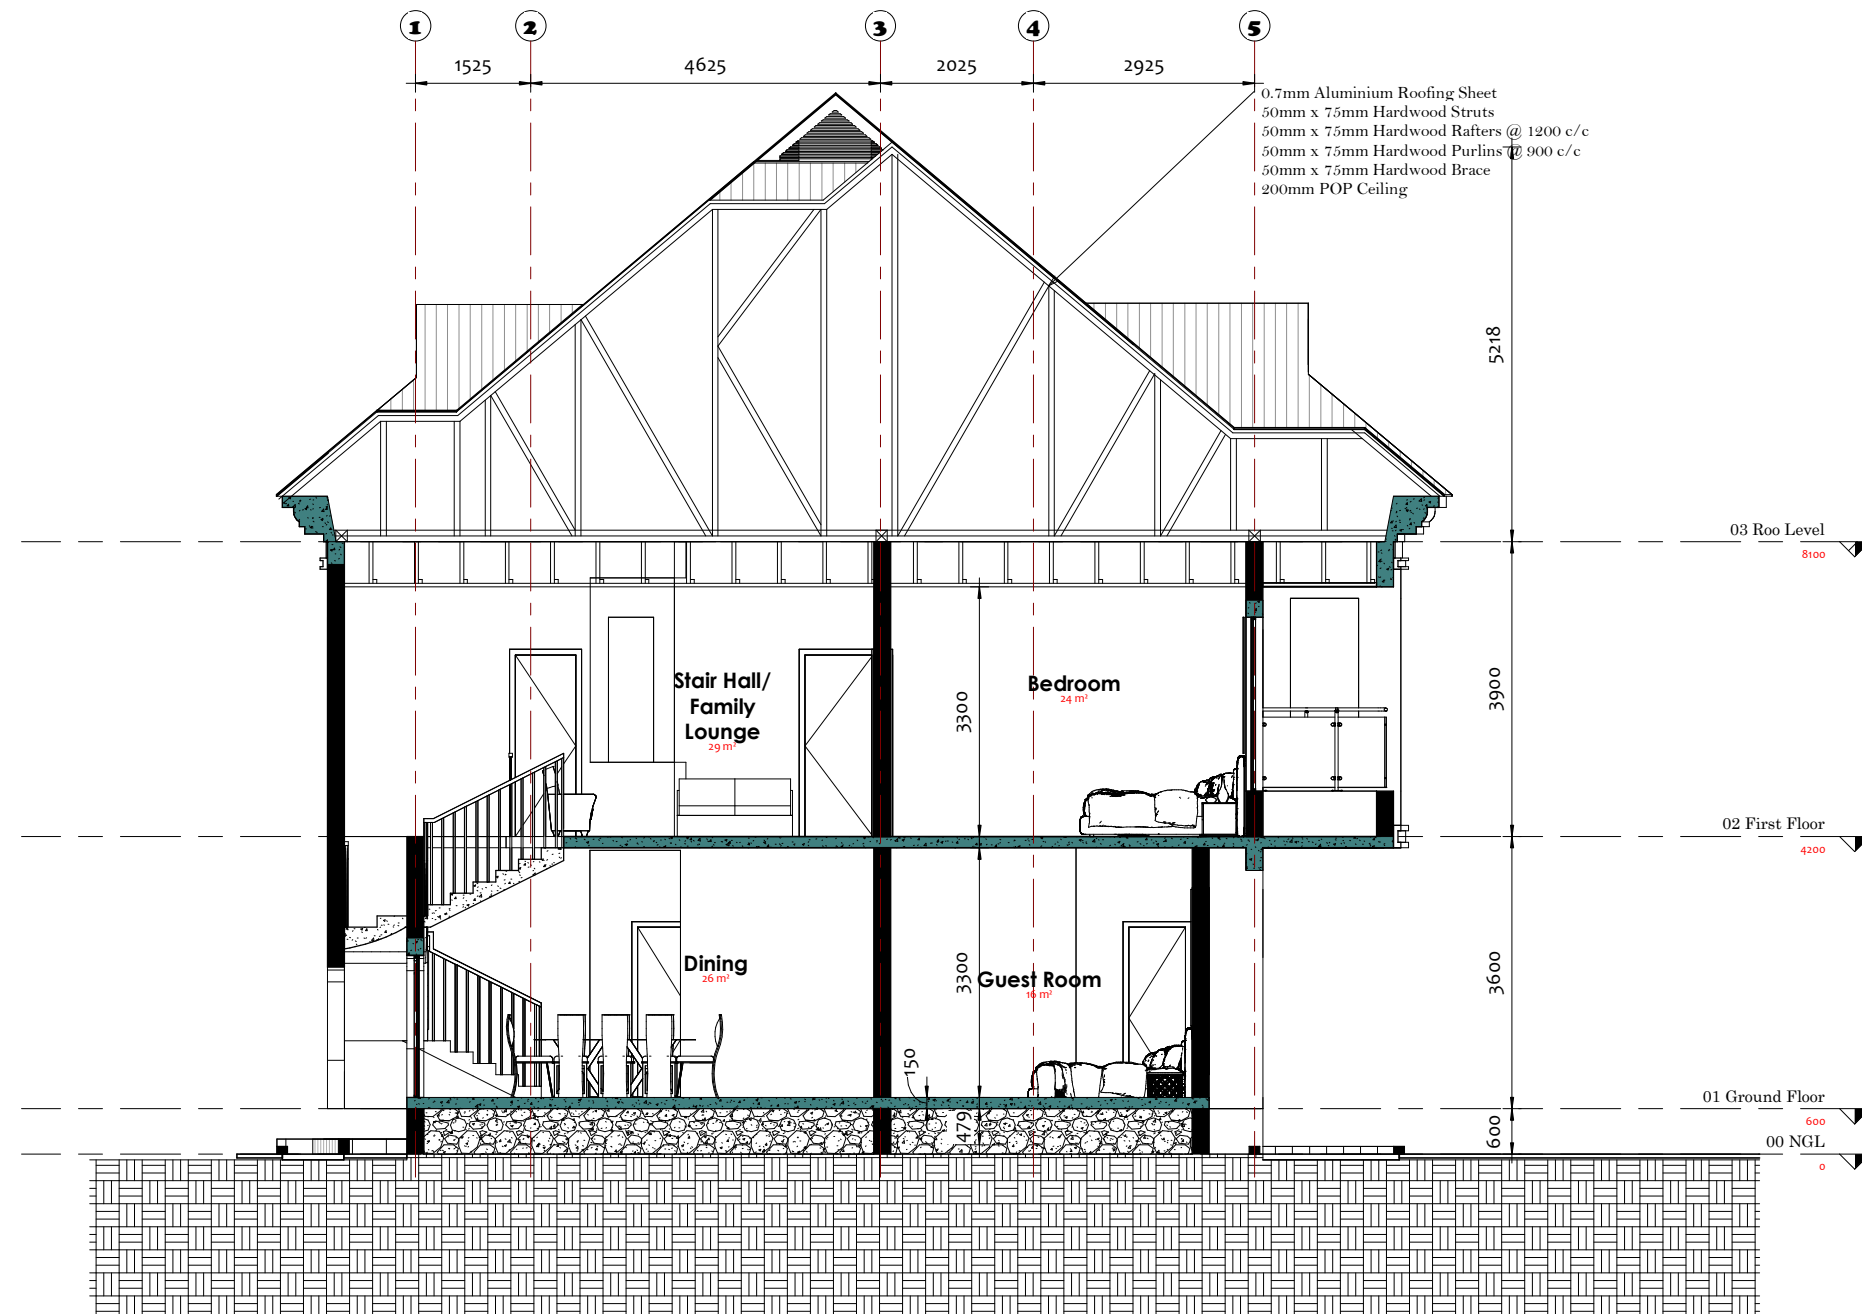


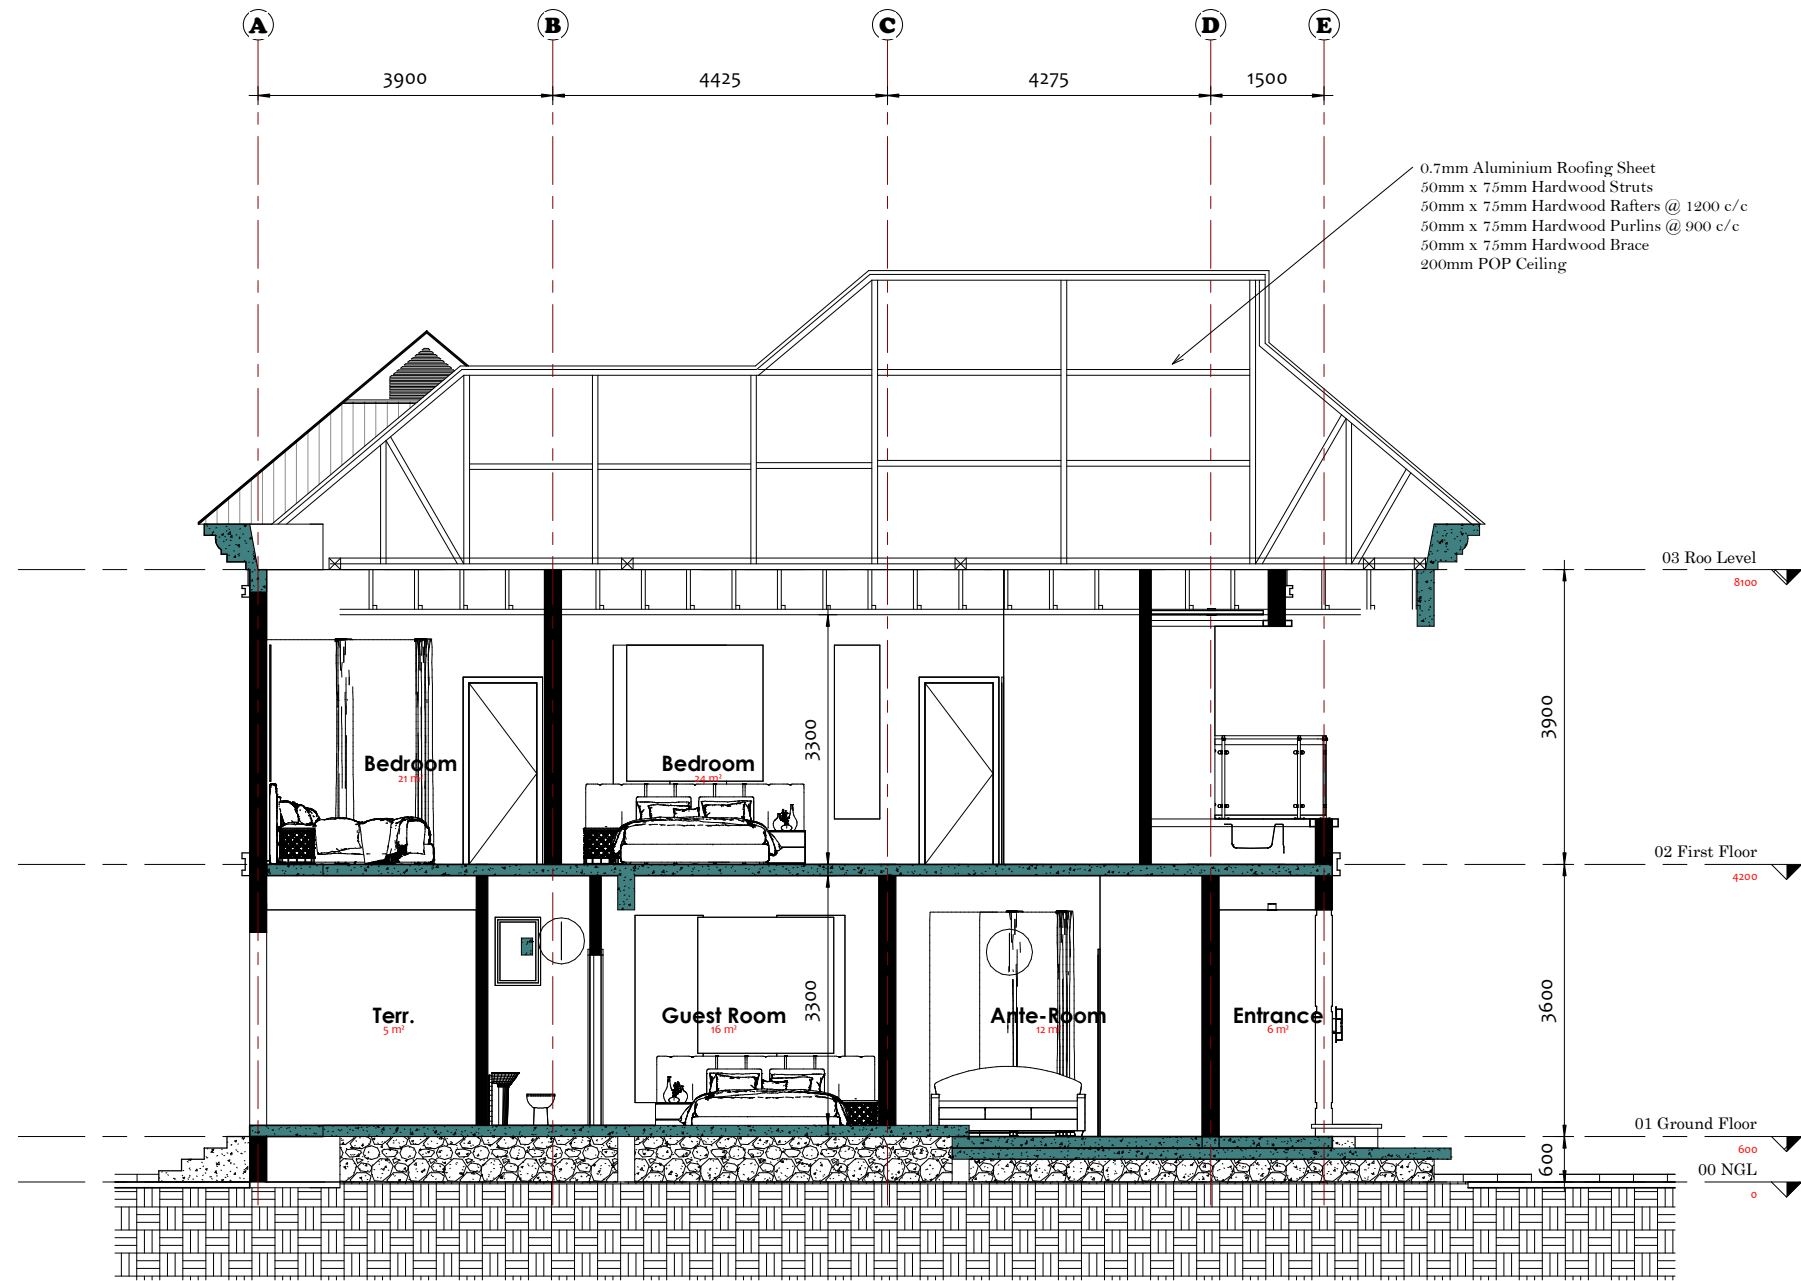


1 Section 2  
1 : 50

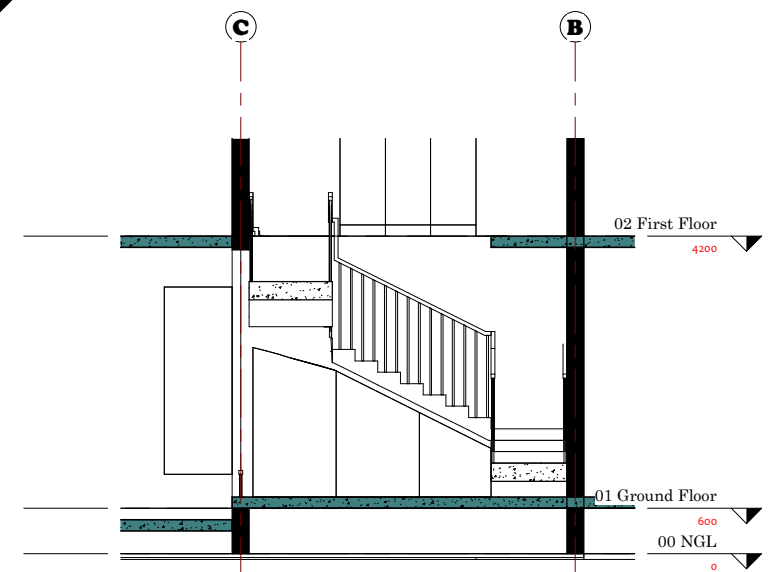

2 Section 3  
1 : 50

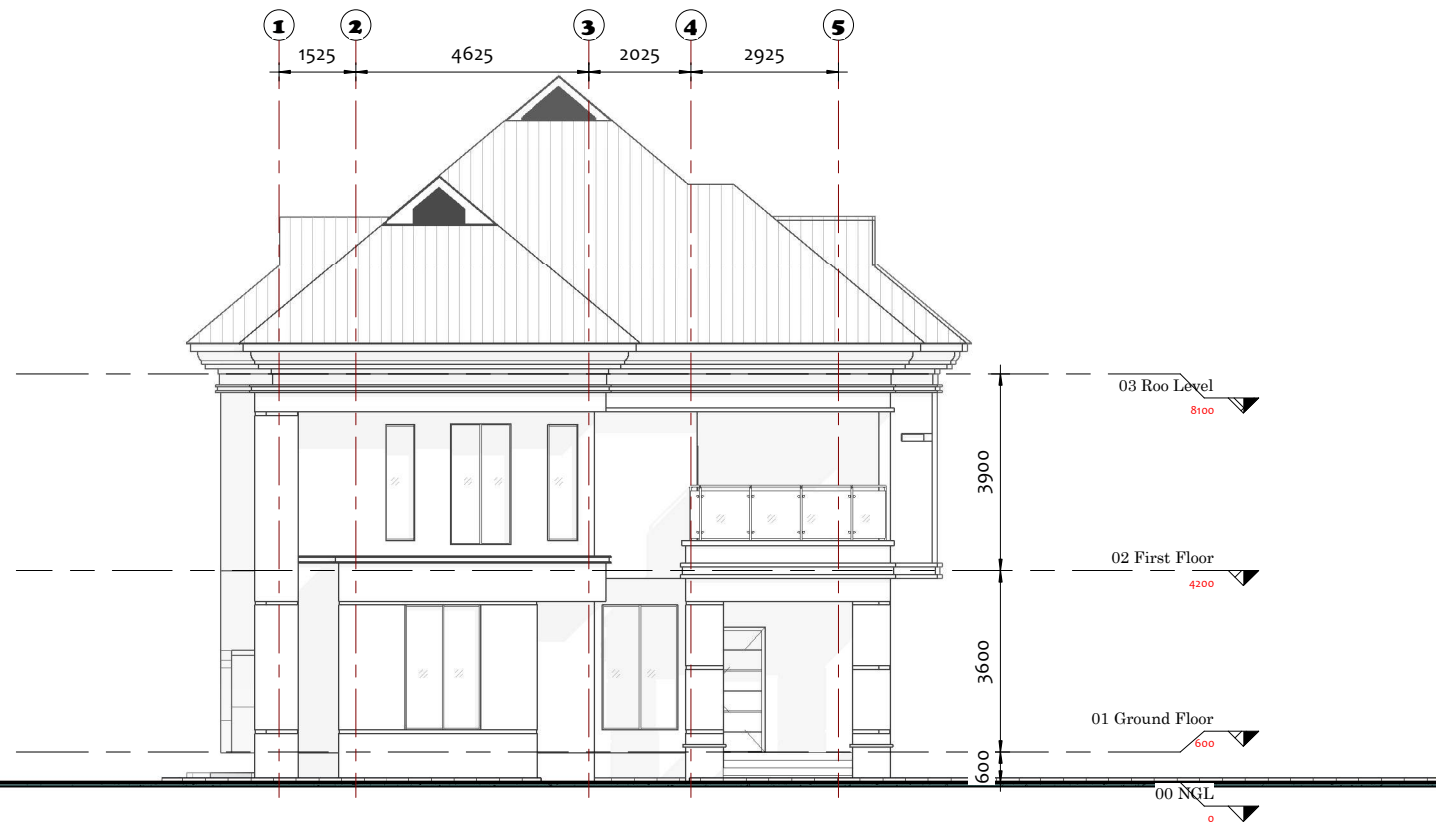


1 00 Approach View  
1 : 75

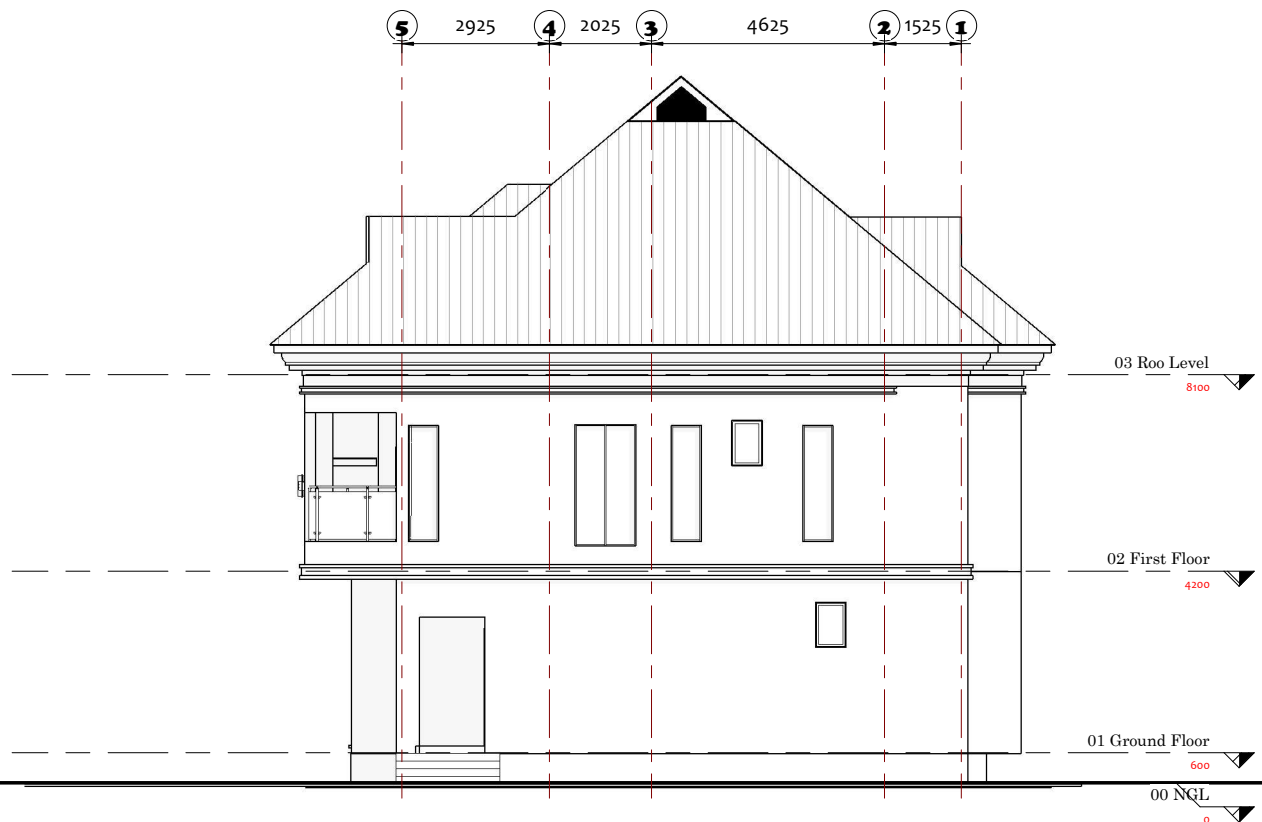

2 01 Rear Elevation  
1 : 75



1 02 RIGHT SIDE  
ELEVATION  
1 : 75

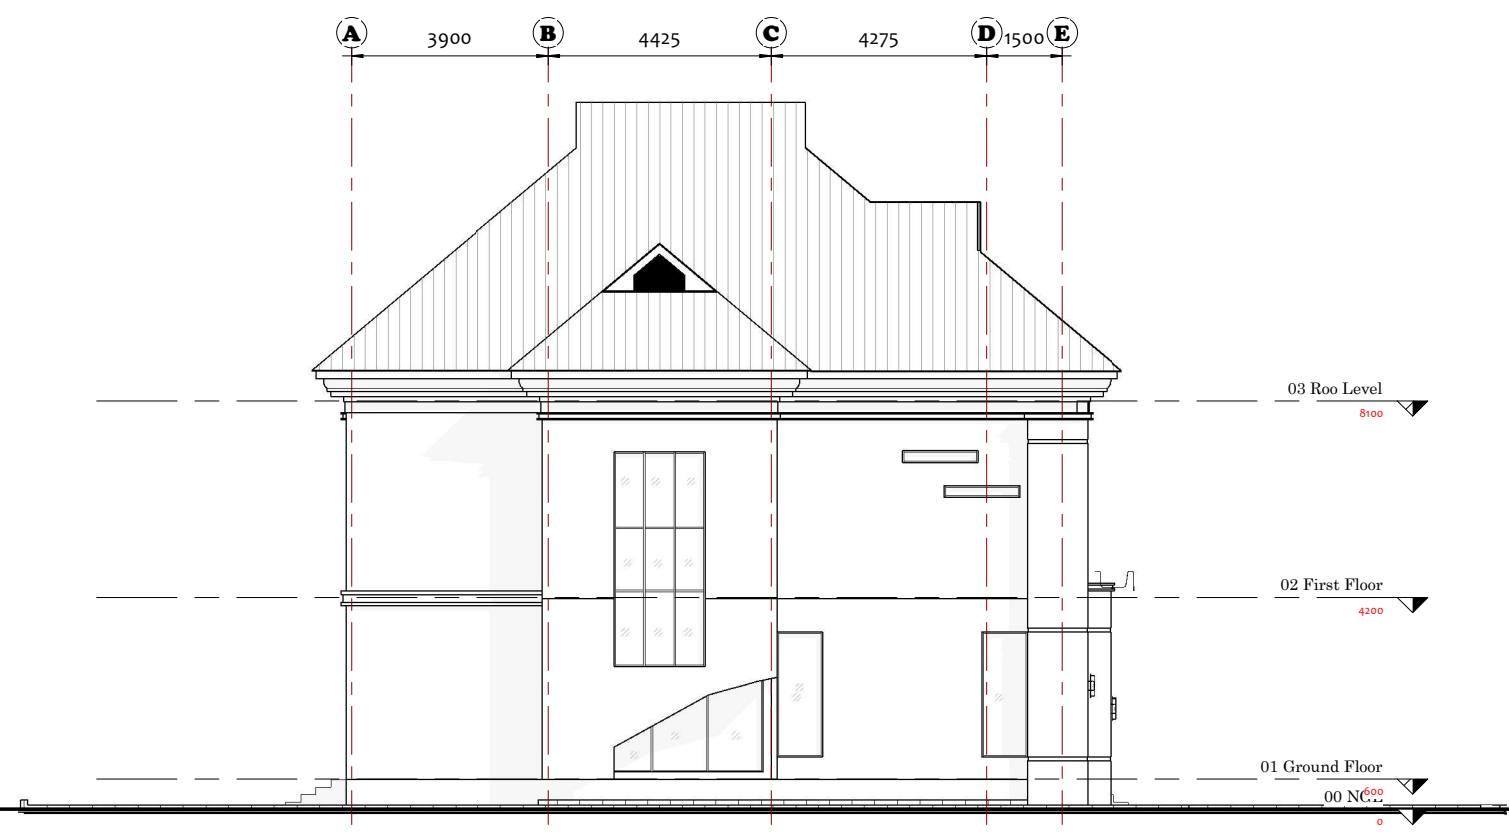

2 03 LEFT SIDE ELEVATION  
1 : 75

WOODEN PANEL DOOR (D-01) 900X2100mm		WOODEN PANEL DOOR (D-02) 750X2100mm		D3 SWISS SECURITY DOOR (D-03) 2100X2100mm	
DOOR DESCRIPTION	Single leaf wooden panel door installed with mortise lock & Architrave on both side	DOOR DESCRIPTION	Single Leaf Wooden internal door installed with mortise lock & Architrave on both sides	DOOR DESCRIPTION	Double Leaf Swiss Security steel door installed with mortise lock & Architrave on both sides
No(s)	09 3608	No(s)	06	No(s)	01