

① Ground floor plan
1 : 100




PROJECT
PROPOSED 4 BEDROOM
DUPLEX

D'PLUZ CONCEPTS
TECHNOLOGIES/ENTERPRISES
08164342535/08155955152

SHEET CONTENT
**GROUND FLOOR
PLAN**

DESIGNED BY	ABDULQUDUS
DRAFTED BY	ABDULQUDUS
CHECKED BY	
SCALE	
DATE	JUNE 2025

02

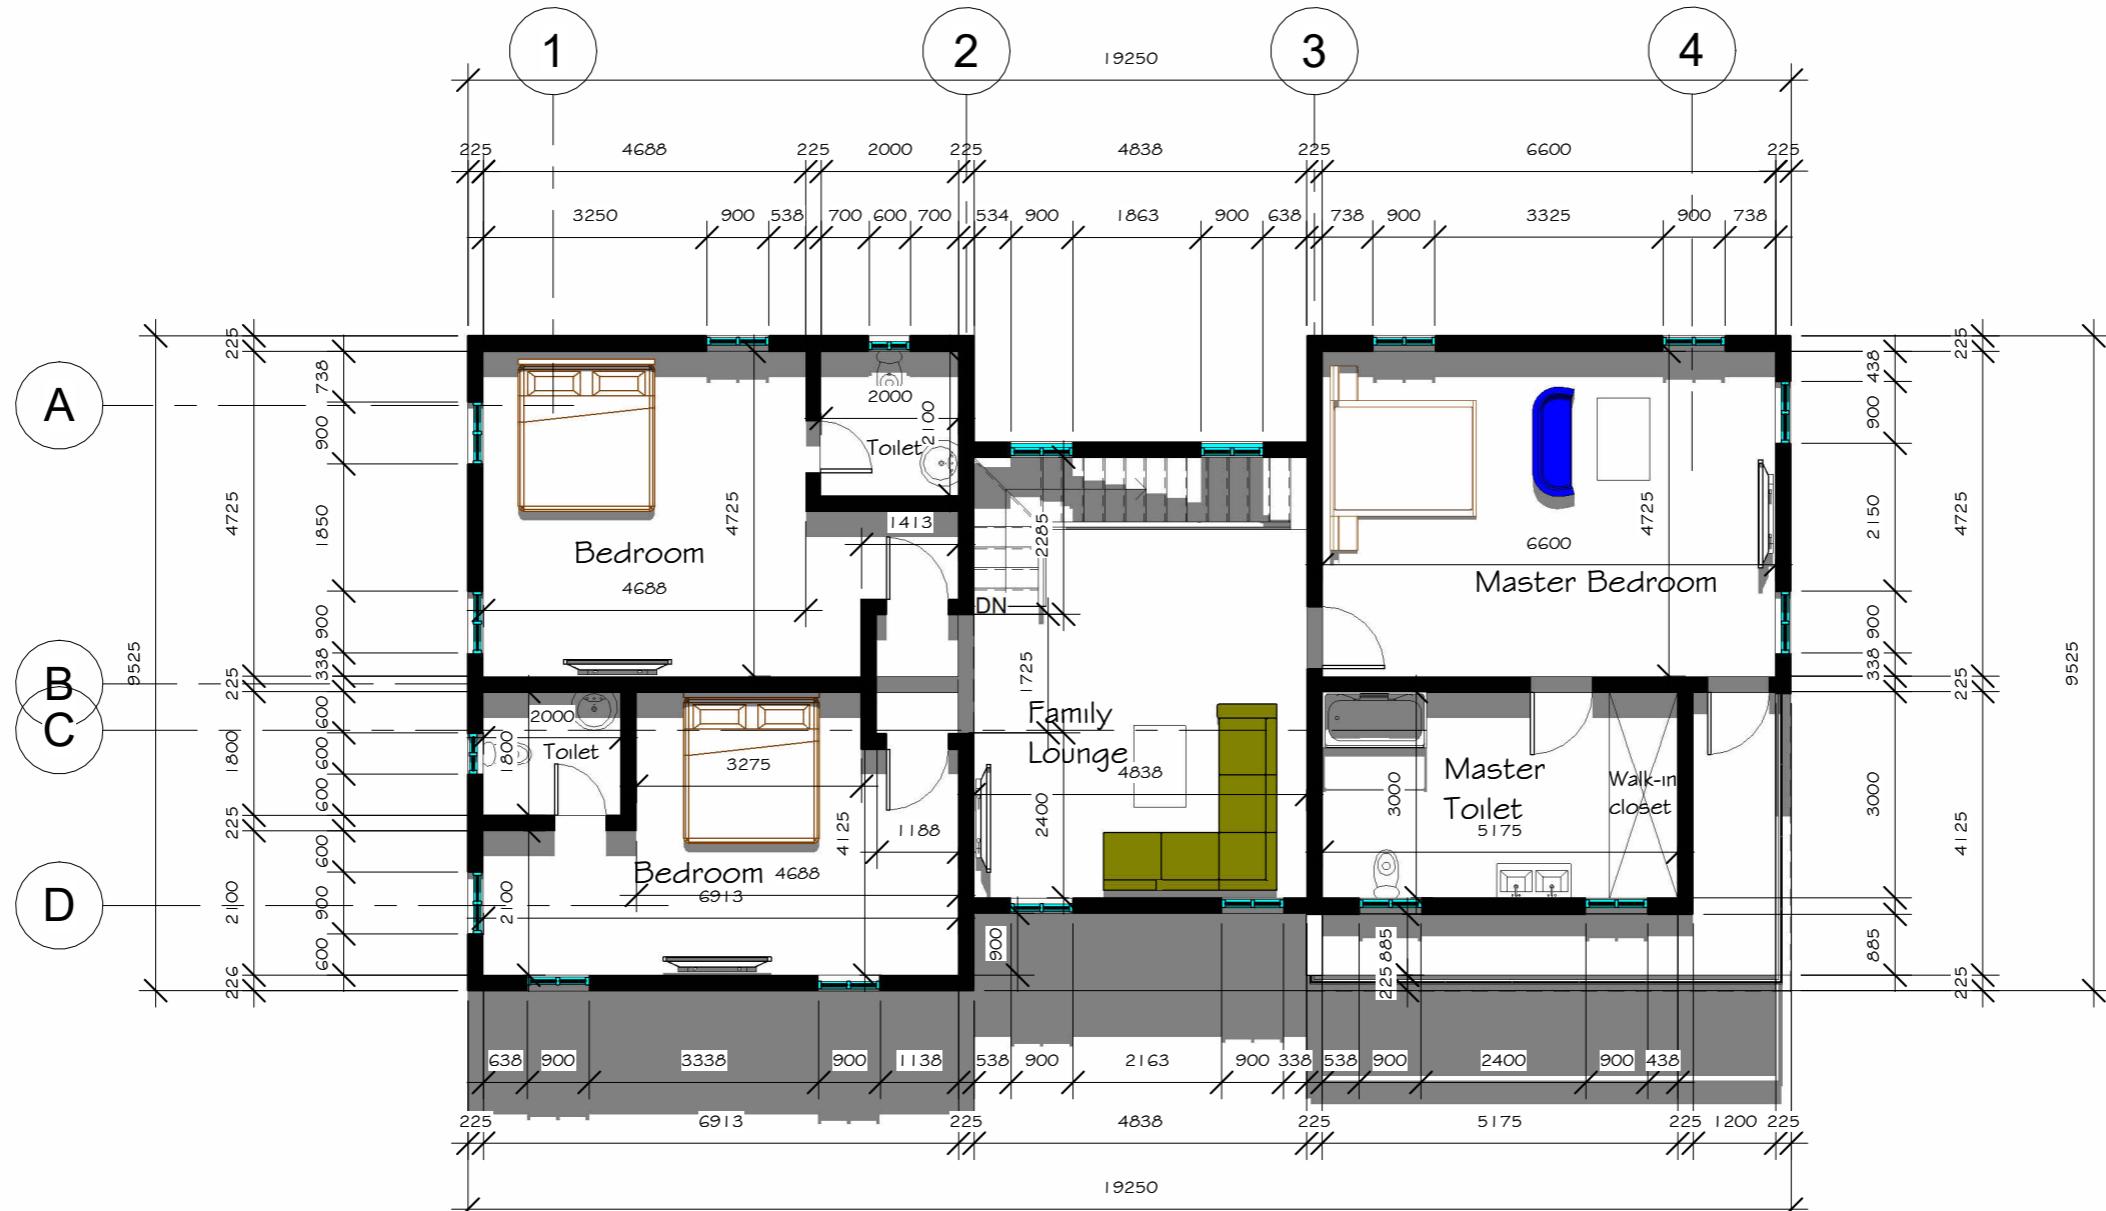

① First floor plan
1 : 100




PROJECT
PROPOSED 4 BEDROOM
DUPLEX

D'PLUZ CONCEPTS
TECHNOLOGIES/ENTERPRISES
08164342535/08155955152

SHEET CONTENT
FIRST FLOOR
PLAN

DESIGNED BY	ABDULQUDUS
DRAFTED BY	ABDULQUDUS
CHECKED BY	
SCALE	
DATE	JUNE 2025

03

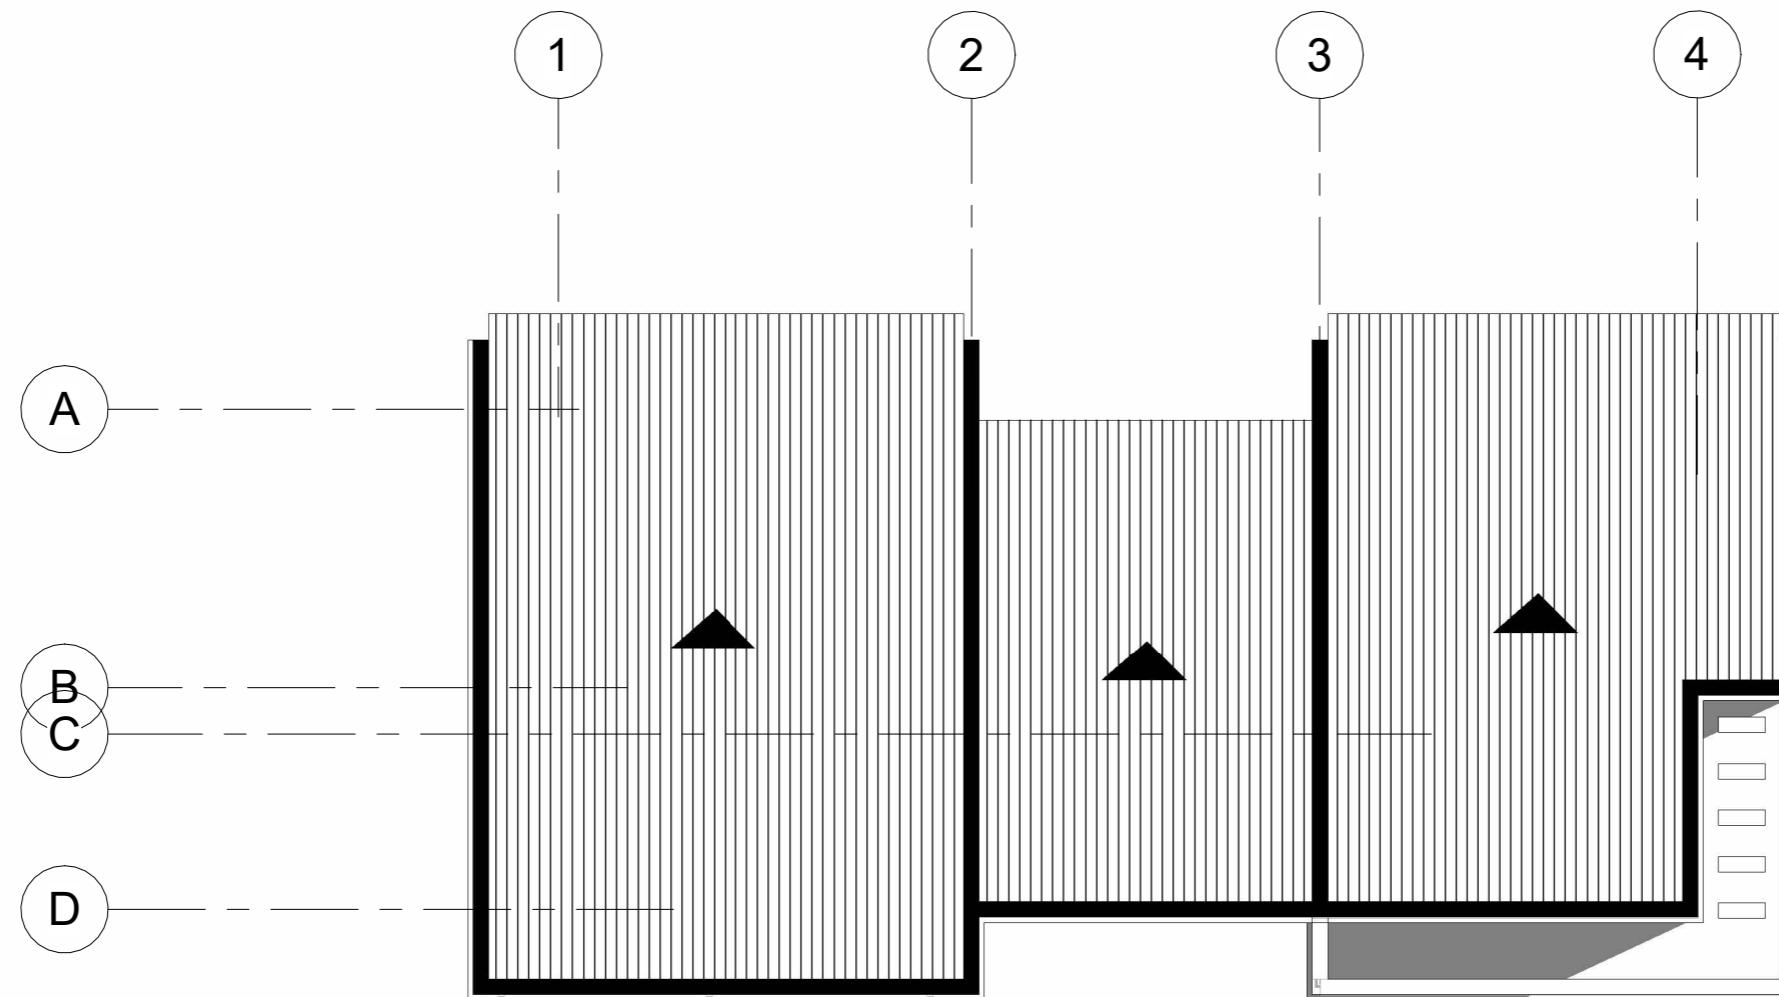

① Roof plan
1 : 100




PROJECT
PROPOSED 4 BEDROOM
DUPLEX

D'PLUZ CONCEPTS
TECHNOLOGIES/ENTERPRISES
08164342535/08155955152

SHEET CONTENT
ROOF PLAN

DESIGNED BY	ABDULQUDUS
DRAFTED BY	ABDULQUDUS
CHECKED BY	
SCALE	
DATE	JUNE 2025

04

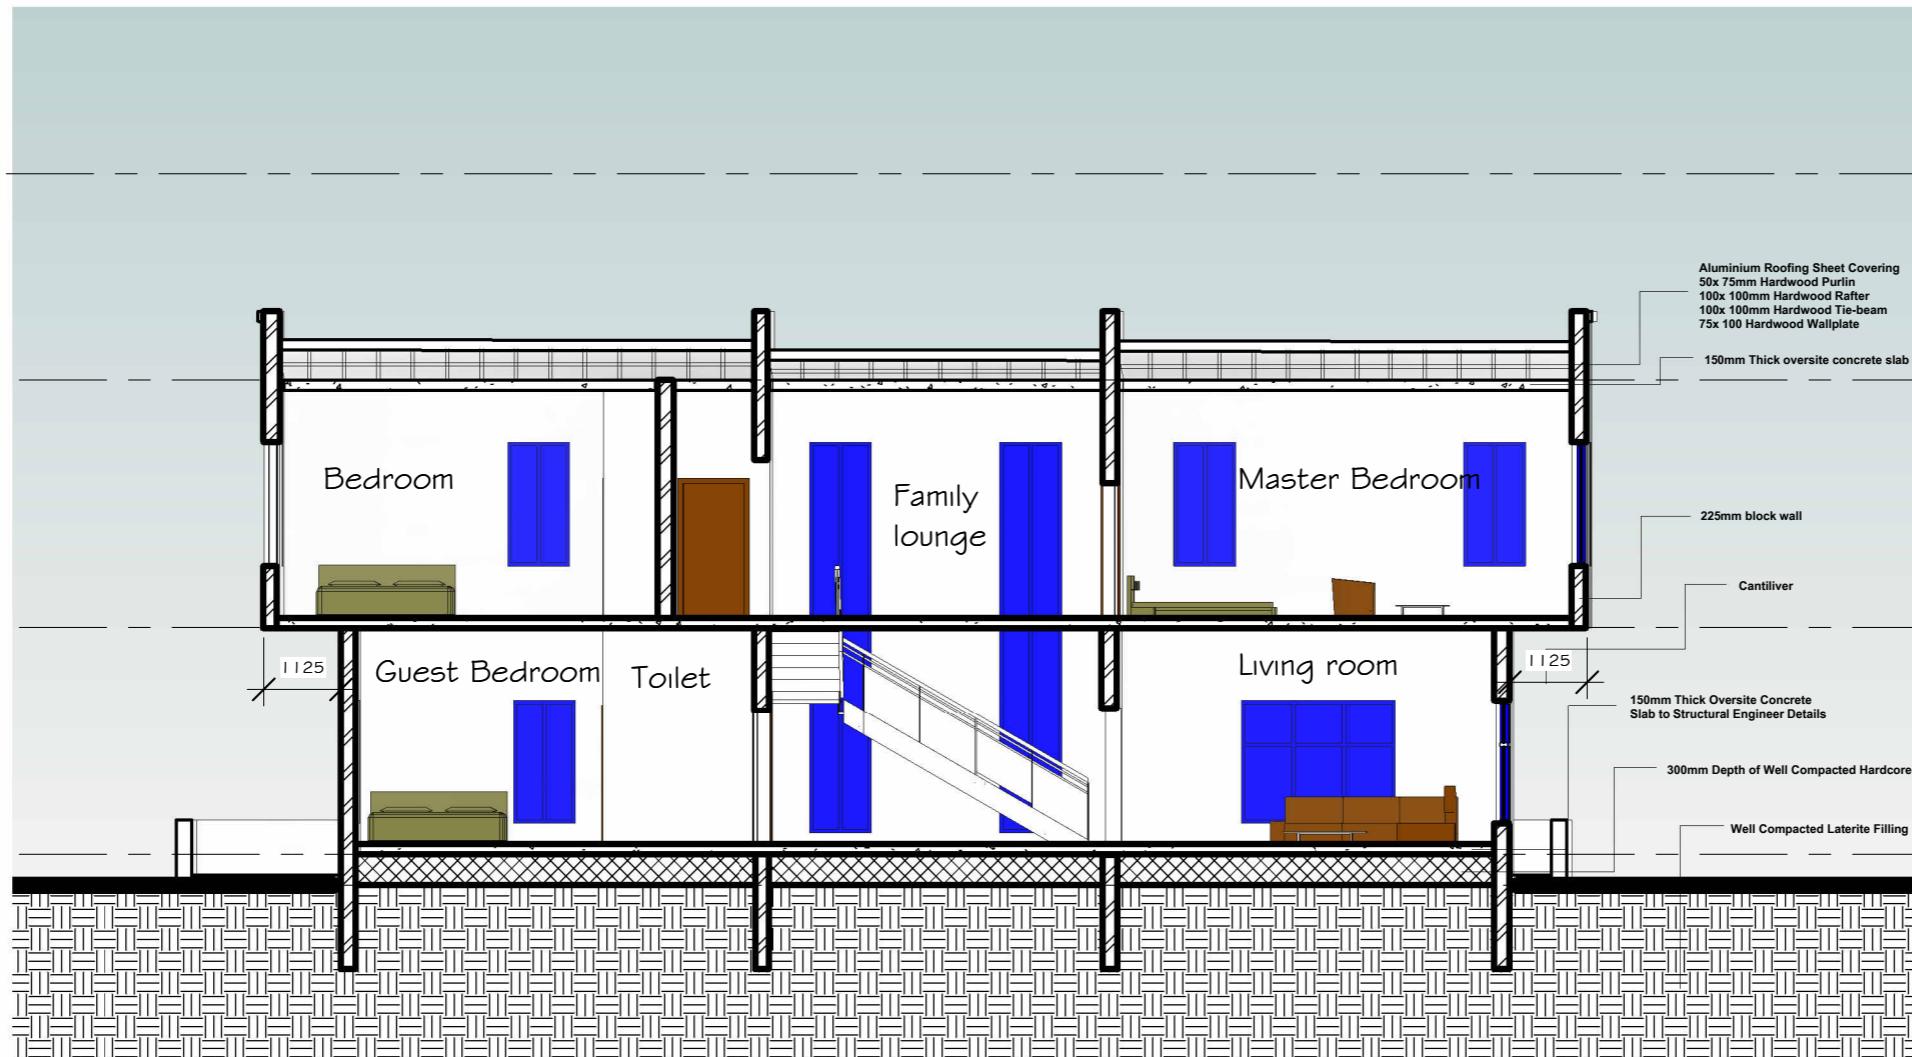

① Section A-A
1 : 100

RFL
10800

Level 4
7800

Level 3
4200

Level 2
Lev900
450

--


PROJECT
PROPOSED 4 BEDROOM
DUPLEX

D'PLUZ CONCEPTS
TECHNOLOGIES/ENTERPRISES
08164342535/08155955152

SHEET CONTENT
SECTION A-A

DESIGNED BY	ABDULQUDUS
DRAFTED BY	ABDULQUDUS
CHECKED BY	
SCALE	
DATE	JUNE 2025

05

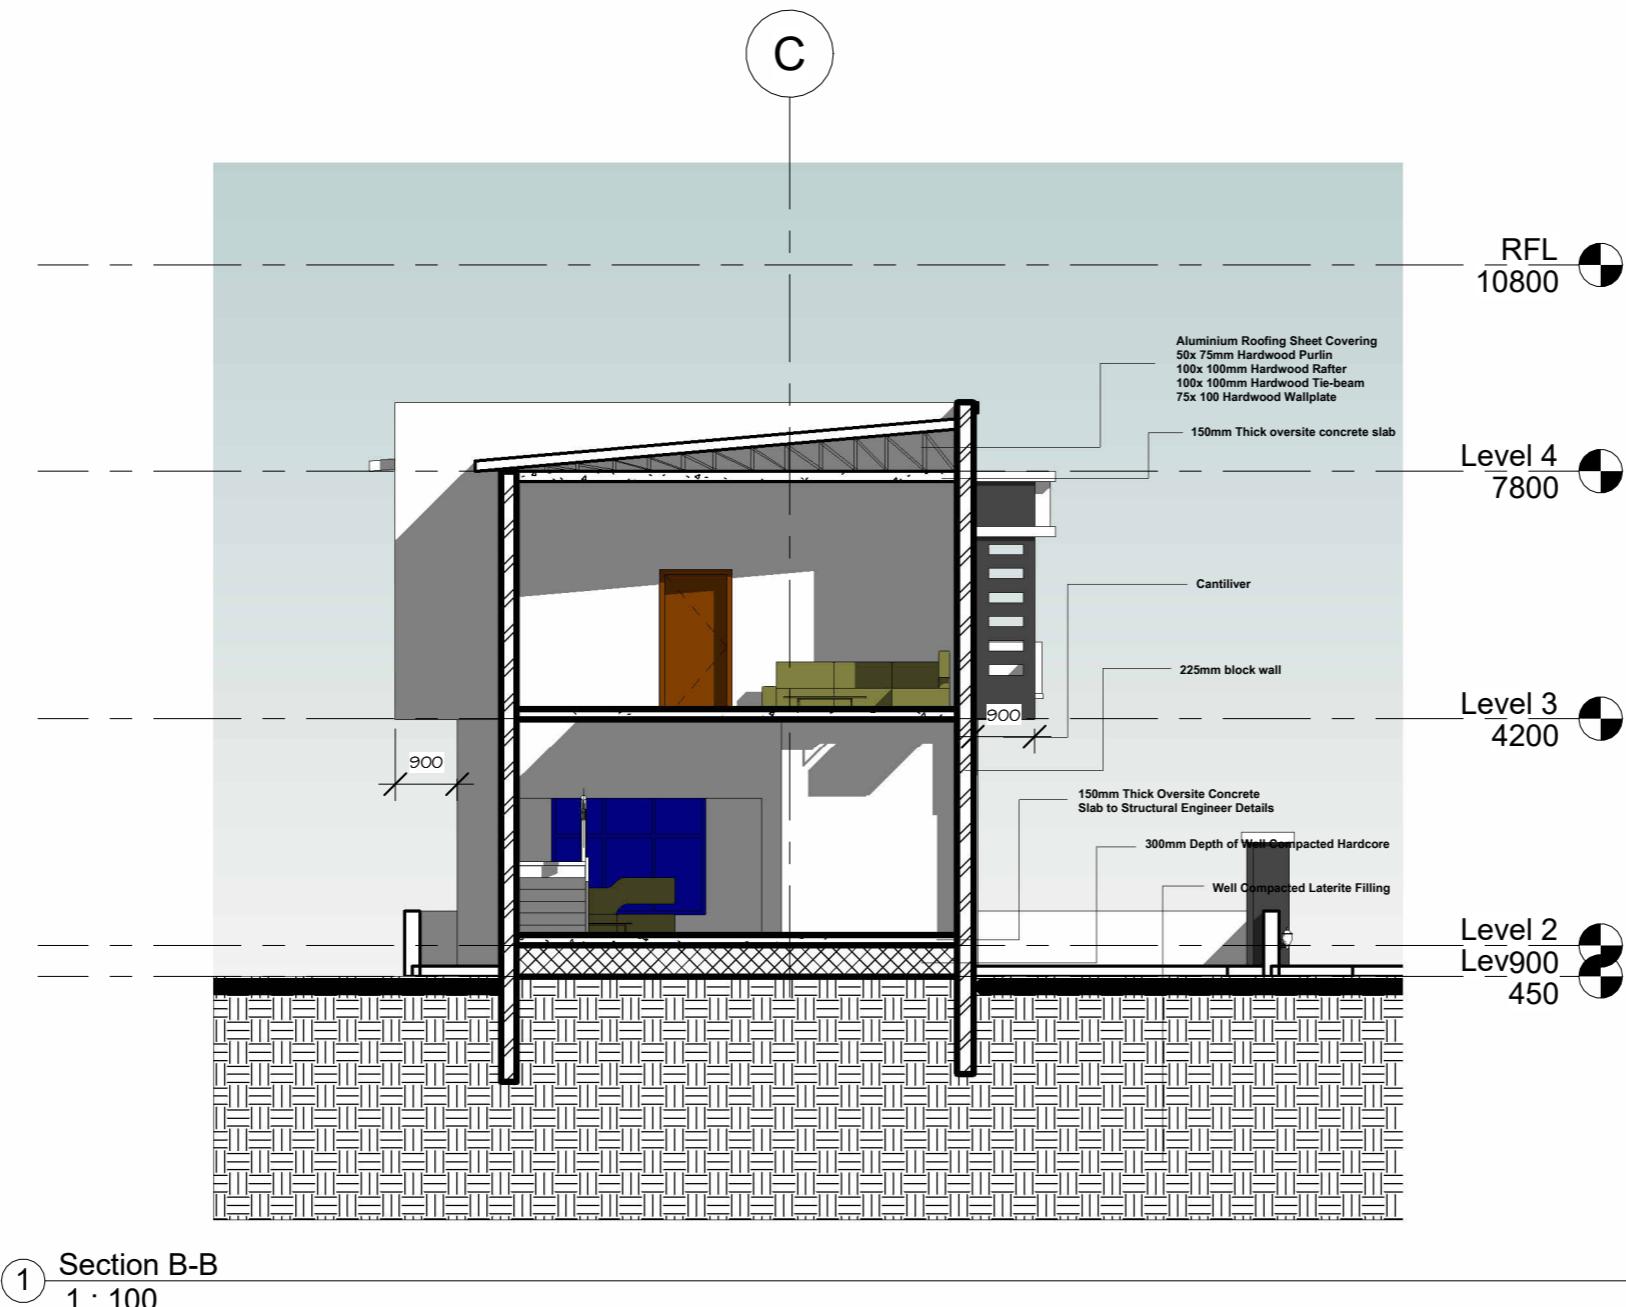

--


PROJECT
PROPOSED 4 BEDROOM
DUPLEX

D'PLUZ CONCEPTS
TECHNOLOGIES/ENTERPRISES
08164342535/08155955152


SHEET CONTENT
SECTION B-B

DESIGNED BY	ABDULQUDUS
DRAFTED BY	ABDULQUDUS
CHECKED BY	
SCALE	
DATE	JUNE 2025

06

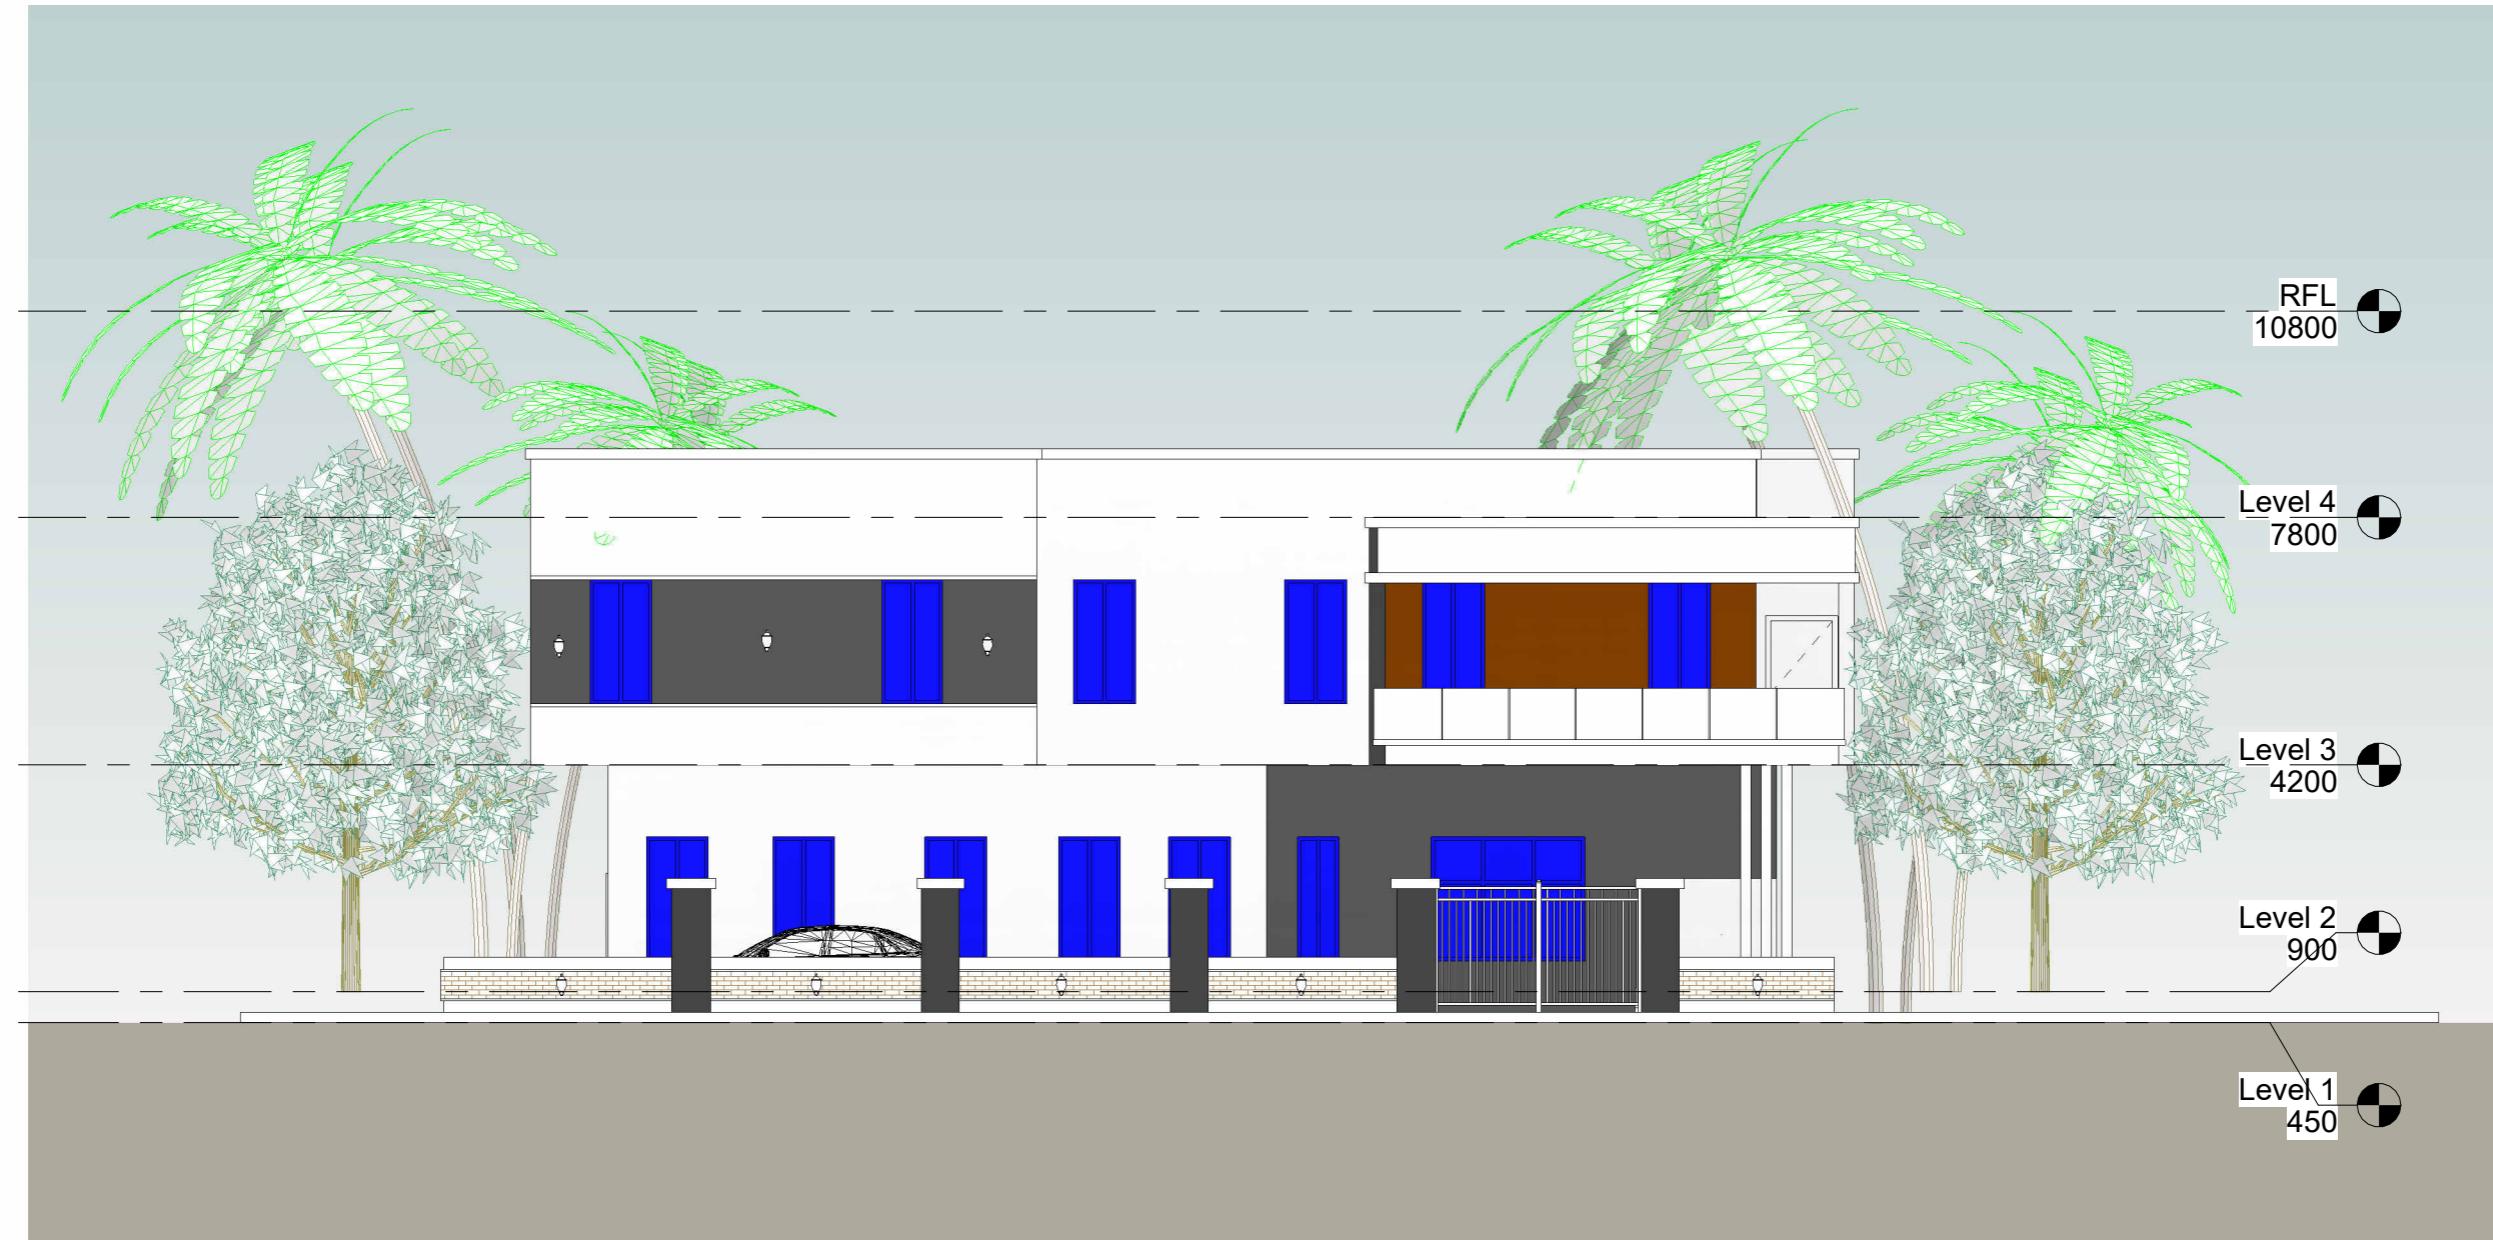

1 Front elevation
1 : 100

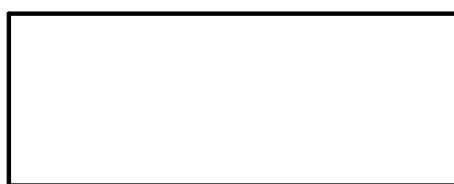

PROJECT
PROPOSED 4 BEDROOM
DUPLEX

D'PLUZ CONCEPTS
TECHNOLOGIES/ENTERPRISES
08164342535/08155955152

SHEET CONTENT
**FRONT
ELEVATION**

DESIGNED BY	ABDULQUDUS
DRAFTED BY	ABDULQUDUS
CHECKED BY	
SCALE	
DATE	JUNE 2025

07



① Right side elevation
1 : 100

--

PROJECT
PROPOSED 4 BEDROOM
DUPLEX

D'PLUZ CONCEPTS
TECHNOLOGIES/ENTERPRISES
08164342535/08155955152

SHEET CONTENT
RIGHT SIDE
ELEVATION

DESIGNED BY	ABDULQUDUS
DRAFTED BY	ABDULQUDUS
CHECKED BY	
SCALE	
DATE	JUNE 2025

08



① Back elevation
1 : 100



PROJECT
PROPOSED 4 BEDROOM
DUPLEX

D'PLUZ CONCEPTS
TECHNOLOGIES/ENTERPRISES
08164342535/08155955152

SHEET CONTENT
**BACK
ELEVATION**

DESIGNED BY	ABDULQUDUS
DRAFTED BY	ABDULQUDUS
CHECKED BY	
SCALE	
DATE	JUNE 2025

09



① Left side elevation
1 : 100



PROJECT
PROPOSED 4 BEDROOM
DUPLEX

D'PLUZ CONCEPTS
TECHNOLOGIES/ENTERPRISES
08164342535/08155955152

SHEET CONTENT
**LEFT SIDE
ELEVATION**

DESIGNED BY	ABDULQUDUS
DRAFTED BY	ABDULQUDUS
CHECKED BY	
SCALE	
DATE	JUNE 2025

10



--

PROJECT
PROPOSED 4 BEDROOM
DUPLEX

D'PLUZ CONCEPTS TECHNOLOGIES/ENTERPRISES 08164342535/08155955152
--

SHEET CONTENT

DESIGNED BY	ABDULQUDUS
DRAFTED BY	ABDULQUDUS
CHECKED BY	
SCALE	
DATE	JUNE 2025

--



PROJECT
PROPOSED 4 BEDROOM
DUPLEX

D'PLUZ CONCEPTS
TECHNOLOGIES/ENTERPRISES
08164342535/08155955152

SHEET CONTENT

DESIGNED BY	ABDULQUDUS
DRAFTED BY	ABDULQUDUS
CHECKED BY	
SCALE	
DATE	JUNE 2025



PROJECT
PROPOSED 4 BEDROOM
DUPLEX

D'PLUZ CONCEPTS
TECHNOLOGIES/ENTERPRISES
08164342535/08155955152

SHEET CONTENT

DESIGNED BY	ABDULQUDUS
DRAFTED BY	ABDULQUDUS
CHECKED BY	
SCALE	
DATE	JUNE 2025